


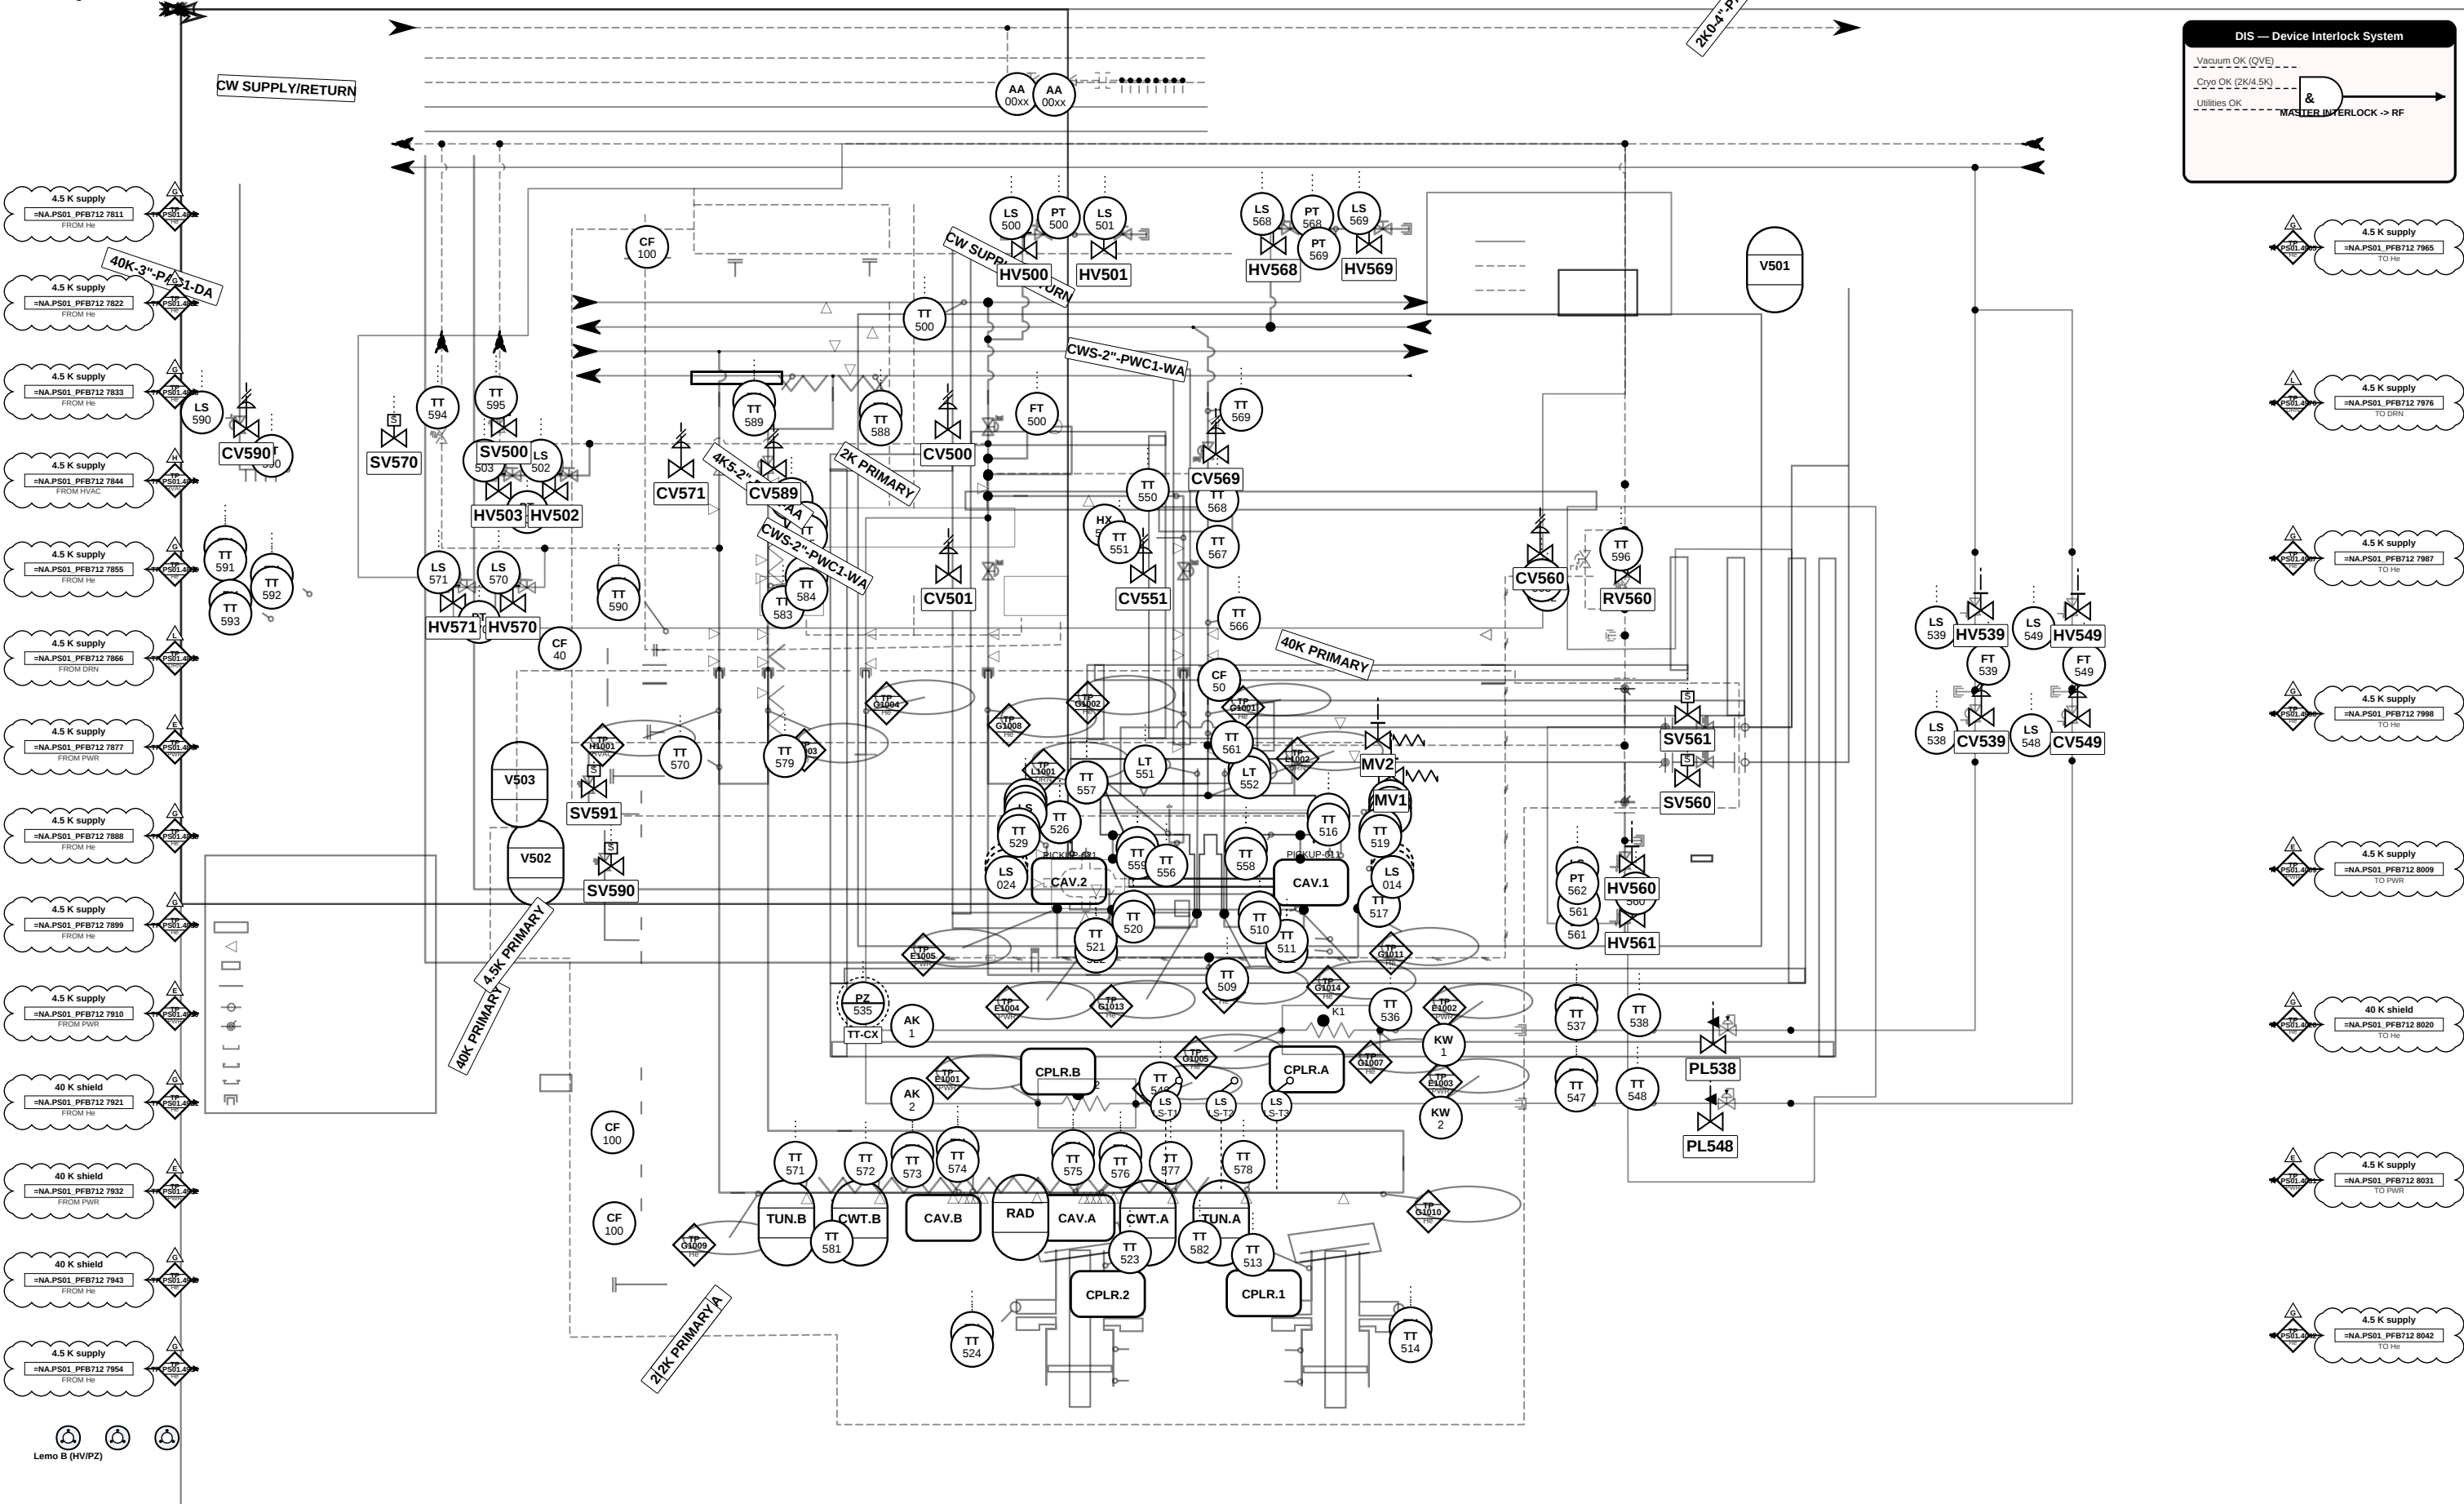

CONSULTANT Mott MacDonald Bristol, UK	CLIENT SCK CEN Boeretang 200, 2400 Mol, BE MYRRHA / MINERVA Phase 1	<table><tr><th>REVISIONS</th><th>Rev</th><th>Date</th><th>Description</th><th>App'd</th></tr><tr><td>C1</td><td></td><td>2026-06</td><td>v3 refinement - layers/legibil</td><td>ACR</td></tr><tr><td>B1</td><td></td><td>2026-05</td><td>v2 split sheets</td><td>ACR</td></tr><tr><td>A1</td><td></td><td>2026-04</td><td>First issue</td><td>ACR</td></tr></table>	REVISIONS	Rev	Date	Description	App'd	C1		2026-06	v3 refinement - layers/legibil	ACR	B1		2026-05	v2 split sheets	ACR	A1		2026-04	First issue	ACR	APPROVALS <table><tr><td>Designed</td><td>QSYS</td></tr><tr><td>Drawn</td><td>ACR</td></tr><tr><td>Checked</td><td>ACR</td></tr><tr><td>Approved</td><td>PM</td></tr></table>	Designed	QSYS	Drawn	ACR	Checked	ACR	Approved	PM	MINERVA CryoCell - SCK CEN QCELL / LB - Instrumentation & Control <table><tr><td>DWG No.</td><td>=NA.PS01_PFB712</td></tr><tr><td>MMD Proj.</td><td>411066</td></tr><tr><td>Scale</td><td>NTS</td></tr><tr><td>Suitability</td><td>S2 - FOR ACCEPTANCE</td></tr><tr><td>Security</td><td>RESTRICTED</td></tr><tr><td>Size / Std</td><td>A3 / ISO10628 / ISA-5.1</td></tr><tr><td>Sheet</td><td>Sheet2 of 2 - Instrumentation</td></tr><tr><td>Variant</td><td>CONTROL-CENTRIC_MONO</td></tr></table>	DWG No.	=NA.PS01_PFB712	MMD Proj.	411066	Scale	NTS	Suitability	S2 - FOR ACCEPTANCE	Security	RESTRICTED	Size / Std	A3 / ISO10628 / ISA-5.1	Sheet	Sheet2 of 2 - Instrumentation	Variant	CONTROL-CENTRIC_MONO
	REVISIONS	Rev	Date	Description	App'd	
	C1		2026-06	v3 refinement - layers/legibil	ACR	
	B1		2026-05	v2 split sheets	ACR	
	A1		2026-04	First issue	ACR	
Designed	QSYS	
Drawn	ACR	
Checked	ACR	
Approved	PM	
DWG No.	=NA.PS01_PFB712	
MMD Proj.	411066	
Scale	NTS	
Suitability	S2 - FOR ACCEPTANCE	
Security	RESTRICTED	
Size / Std	A3 / ISO10628 / ISA-5.1	
Sheet	Sheet2 of 2 - Instrumentation	
Variant	CONTROL-CENTRIC_MONO	