


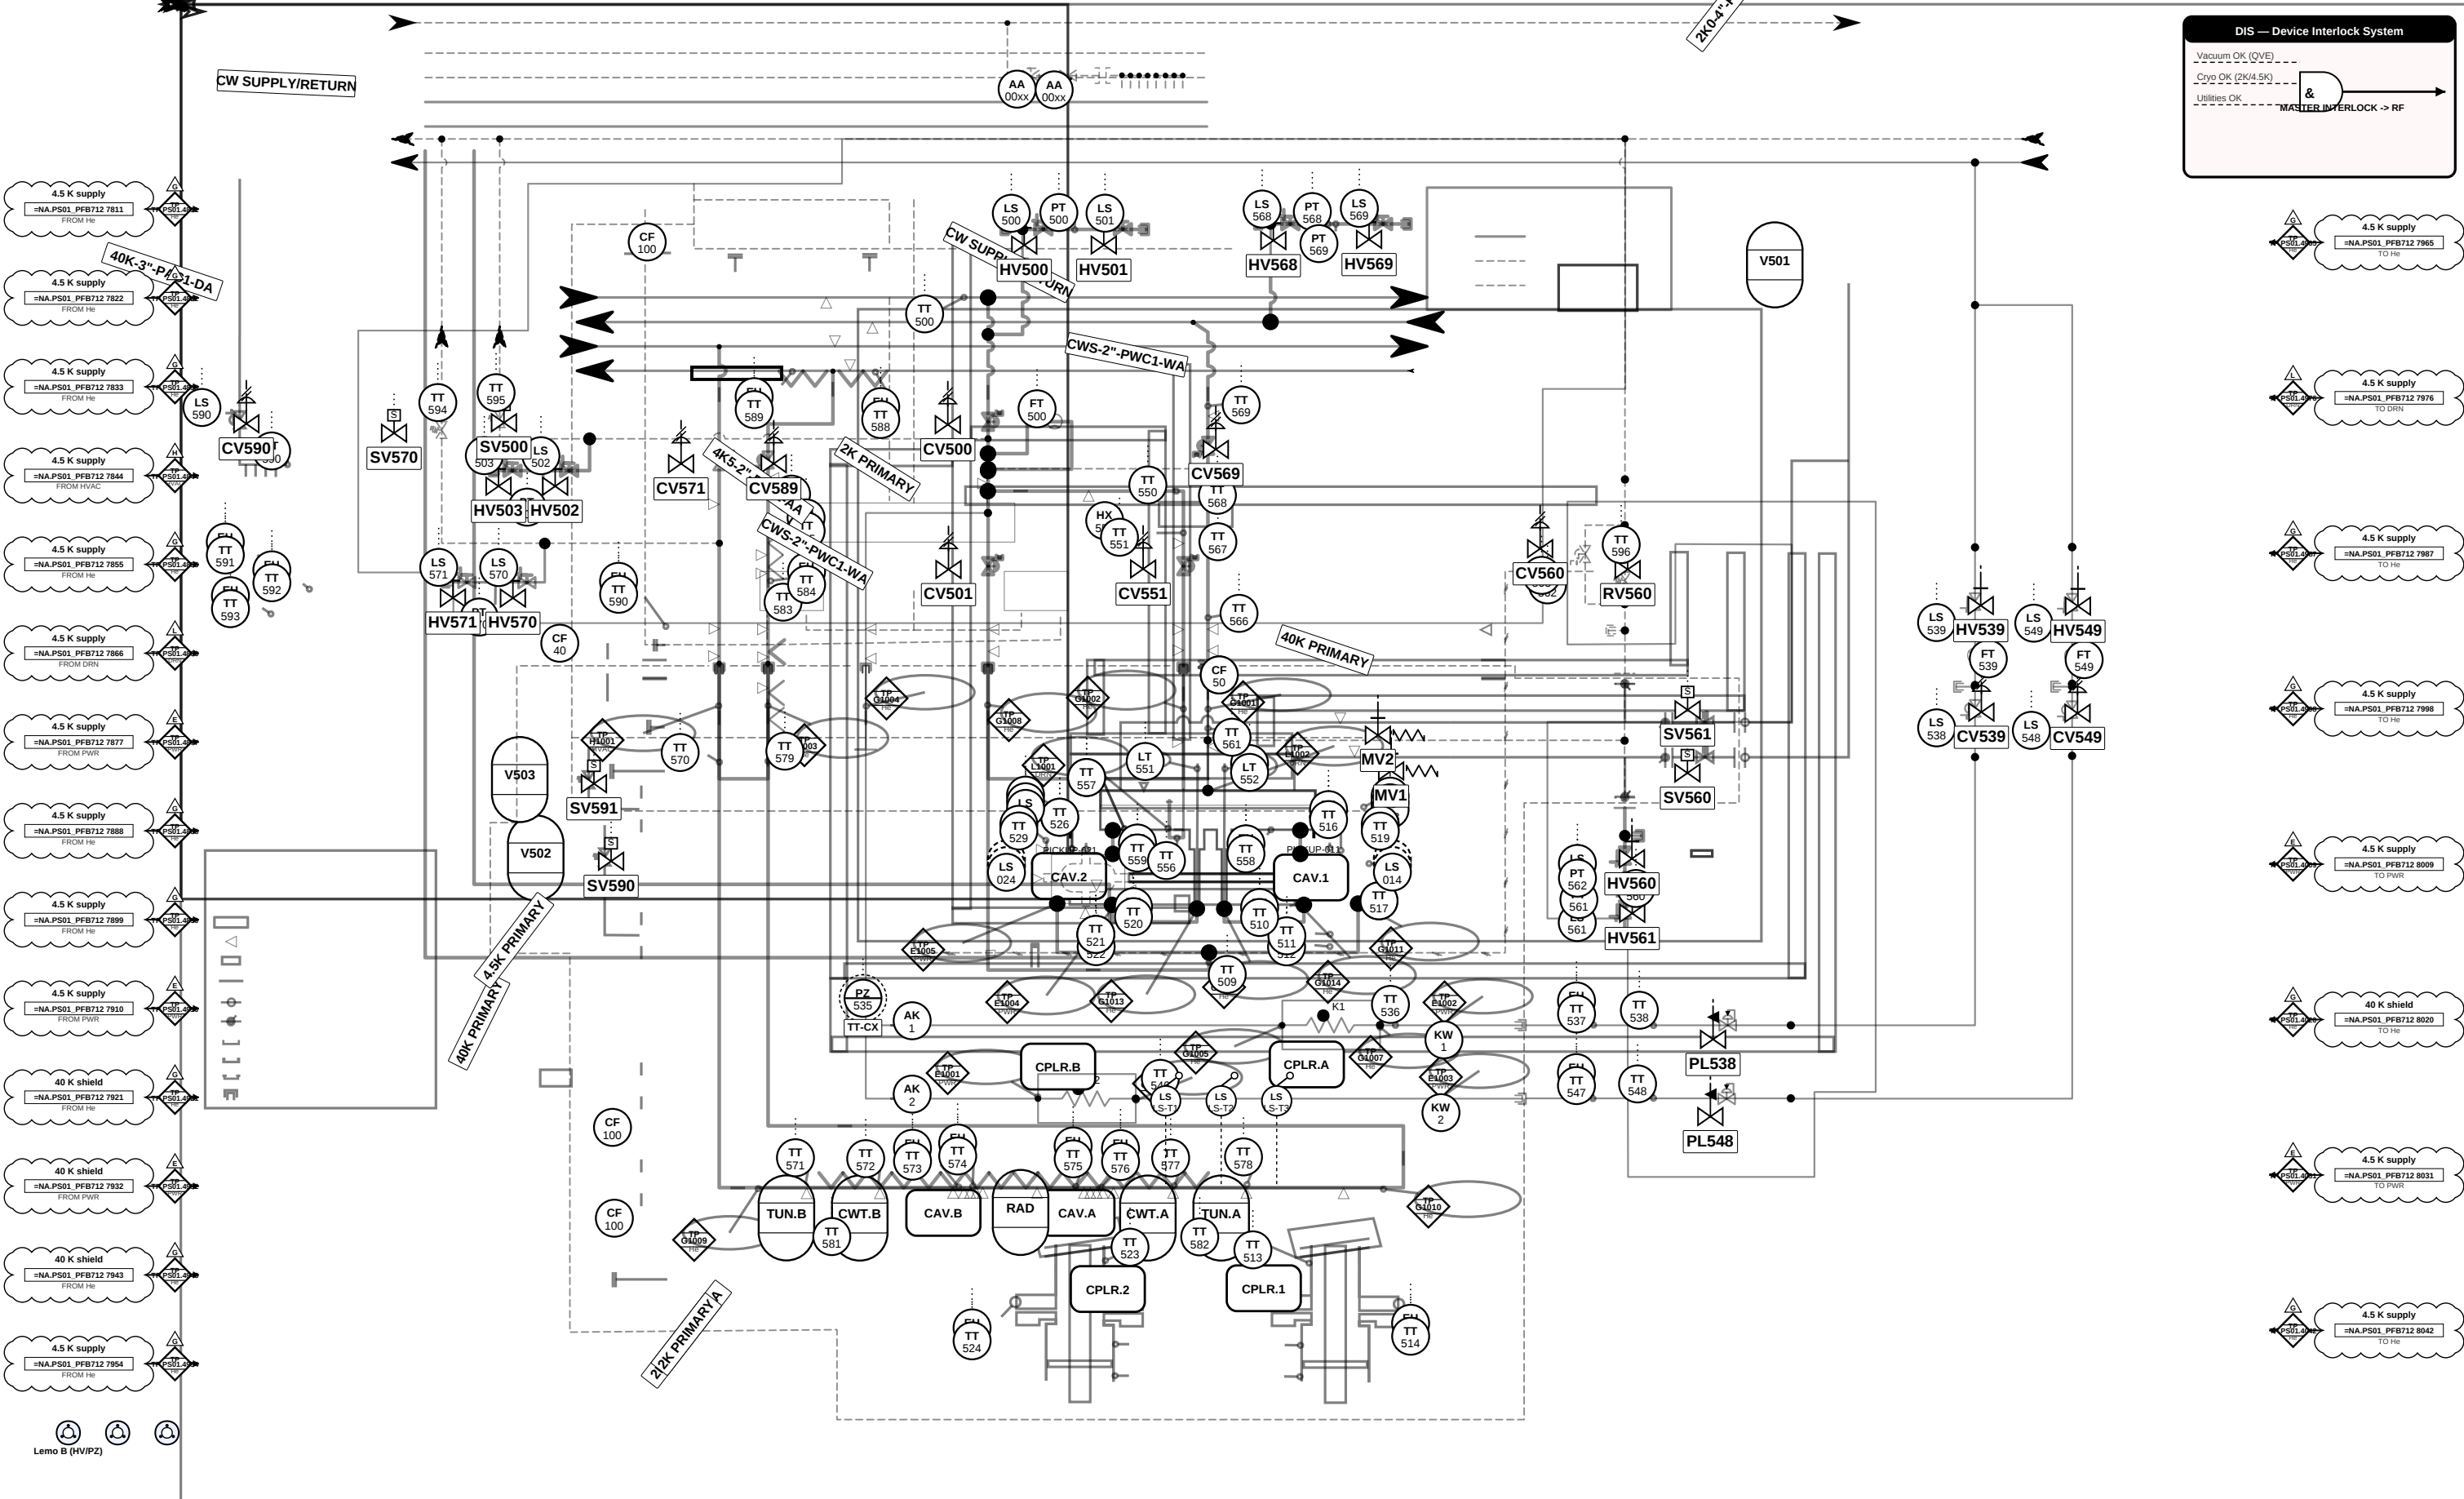

DIS — Device Interlock System

Vacuum OK (QVE) ...
Cryo OK (2K/4.5K) ...
Utilities OK ...

MASTER INTERLOCK -> RF

CONSULTANT Mott MacDonald Bristol, UK	CLIENT SCK CEN Boeretang 200, 2400 Mol, BE MYRRHA / MINERVA Phase 1	<table><tr><th>REVISIONS</th><th>Rev</th><th>Date</th><th>Description</th><th>App'd</th></tr><tr><td>C1</td><td></td><td>2026-06</td><td>v3 refinement - layers/legibil</td><td>ACR</td></tr><tr><td>B1</td><td></td><td>2026-05</td><td>v2 split sheets</td><td>ACR</td></tr><tr><td>A1</td><td></td><td>2026-04</td><td>First issue</td><td>ACR</td></tr></table>	REVISIONS	Rev	Date	Description	App'd	C1		2026-06	v3 refinement - layers/legibil	ACR	B1		2026-05	v2 split sheets	ACR	A1		2026-04	First issue	ACR	APPROVALS Designed QSYS Drawn ACR Checked ACR Approved PM	MINERVA CryoCell - SCK CEN QCELL / LB - Instrumentation & Control DWG No. =NA.PS01_PFB712 MMD Proj. 411066 Scale NTS Suitability S2 - FOR ACCEPTANCE Security RESTRICTED Size / Std A3 / ISO10628 / ISA-5.1 Sheet Sheet2 of 2 - Instrumentation Variant STANDARD_MONO
REVISIONS	Rev	Date	Description	App'd																				
C1		2026-06	v3 refinement - layers/legibil	ACR																				
B1		2026-05	v2 split sheets	ACR																				
A1		2026-04	First issue	ACR																				