


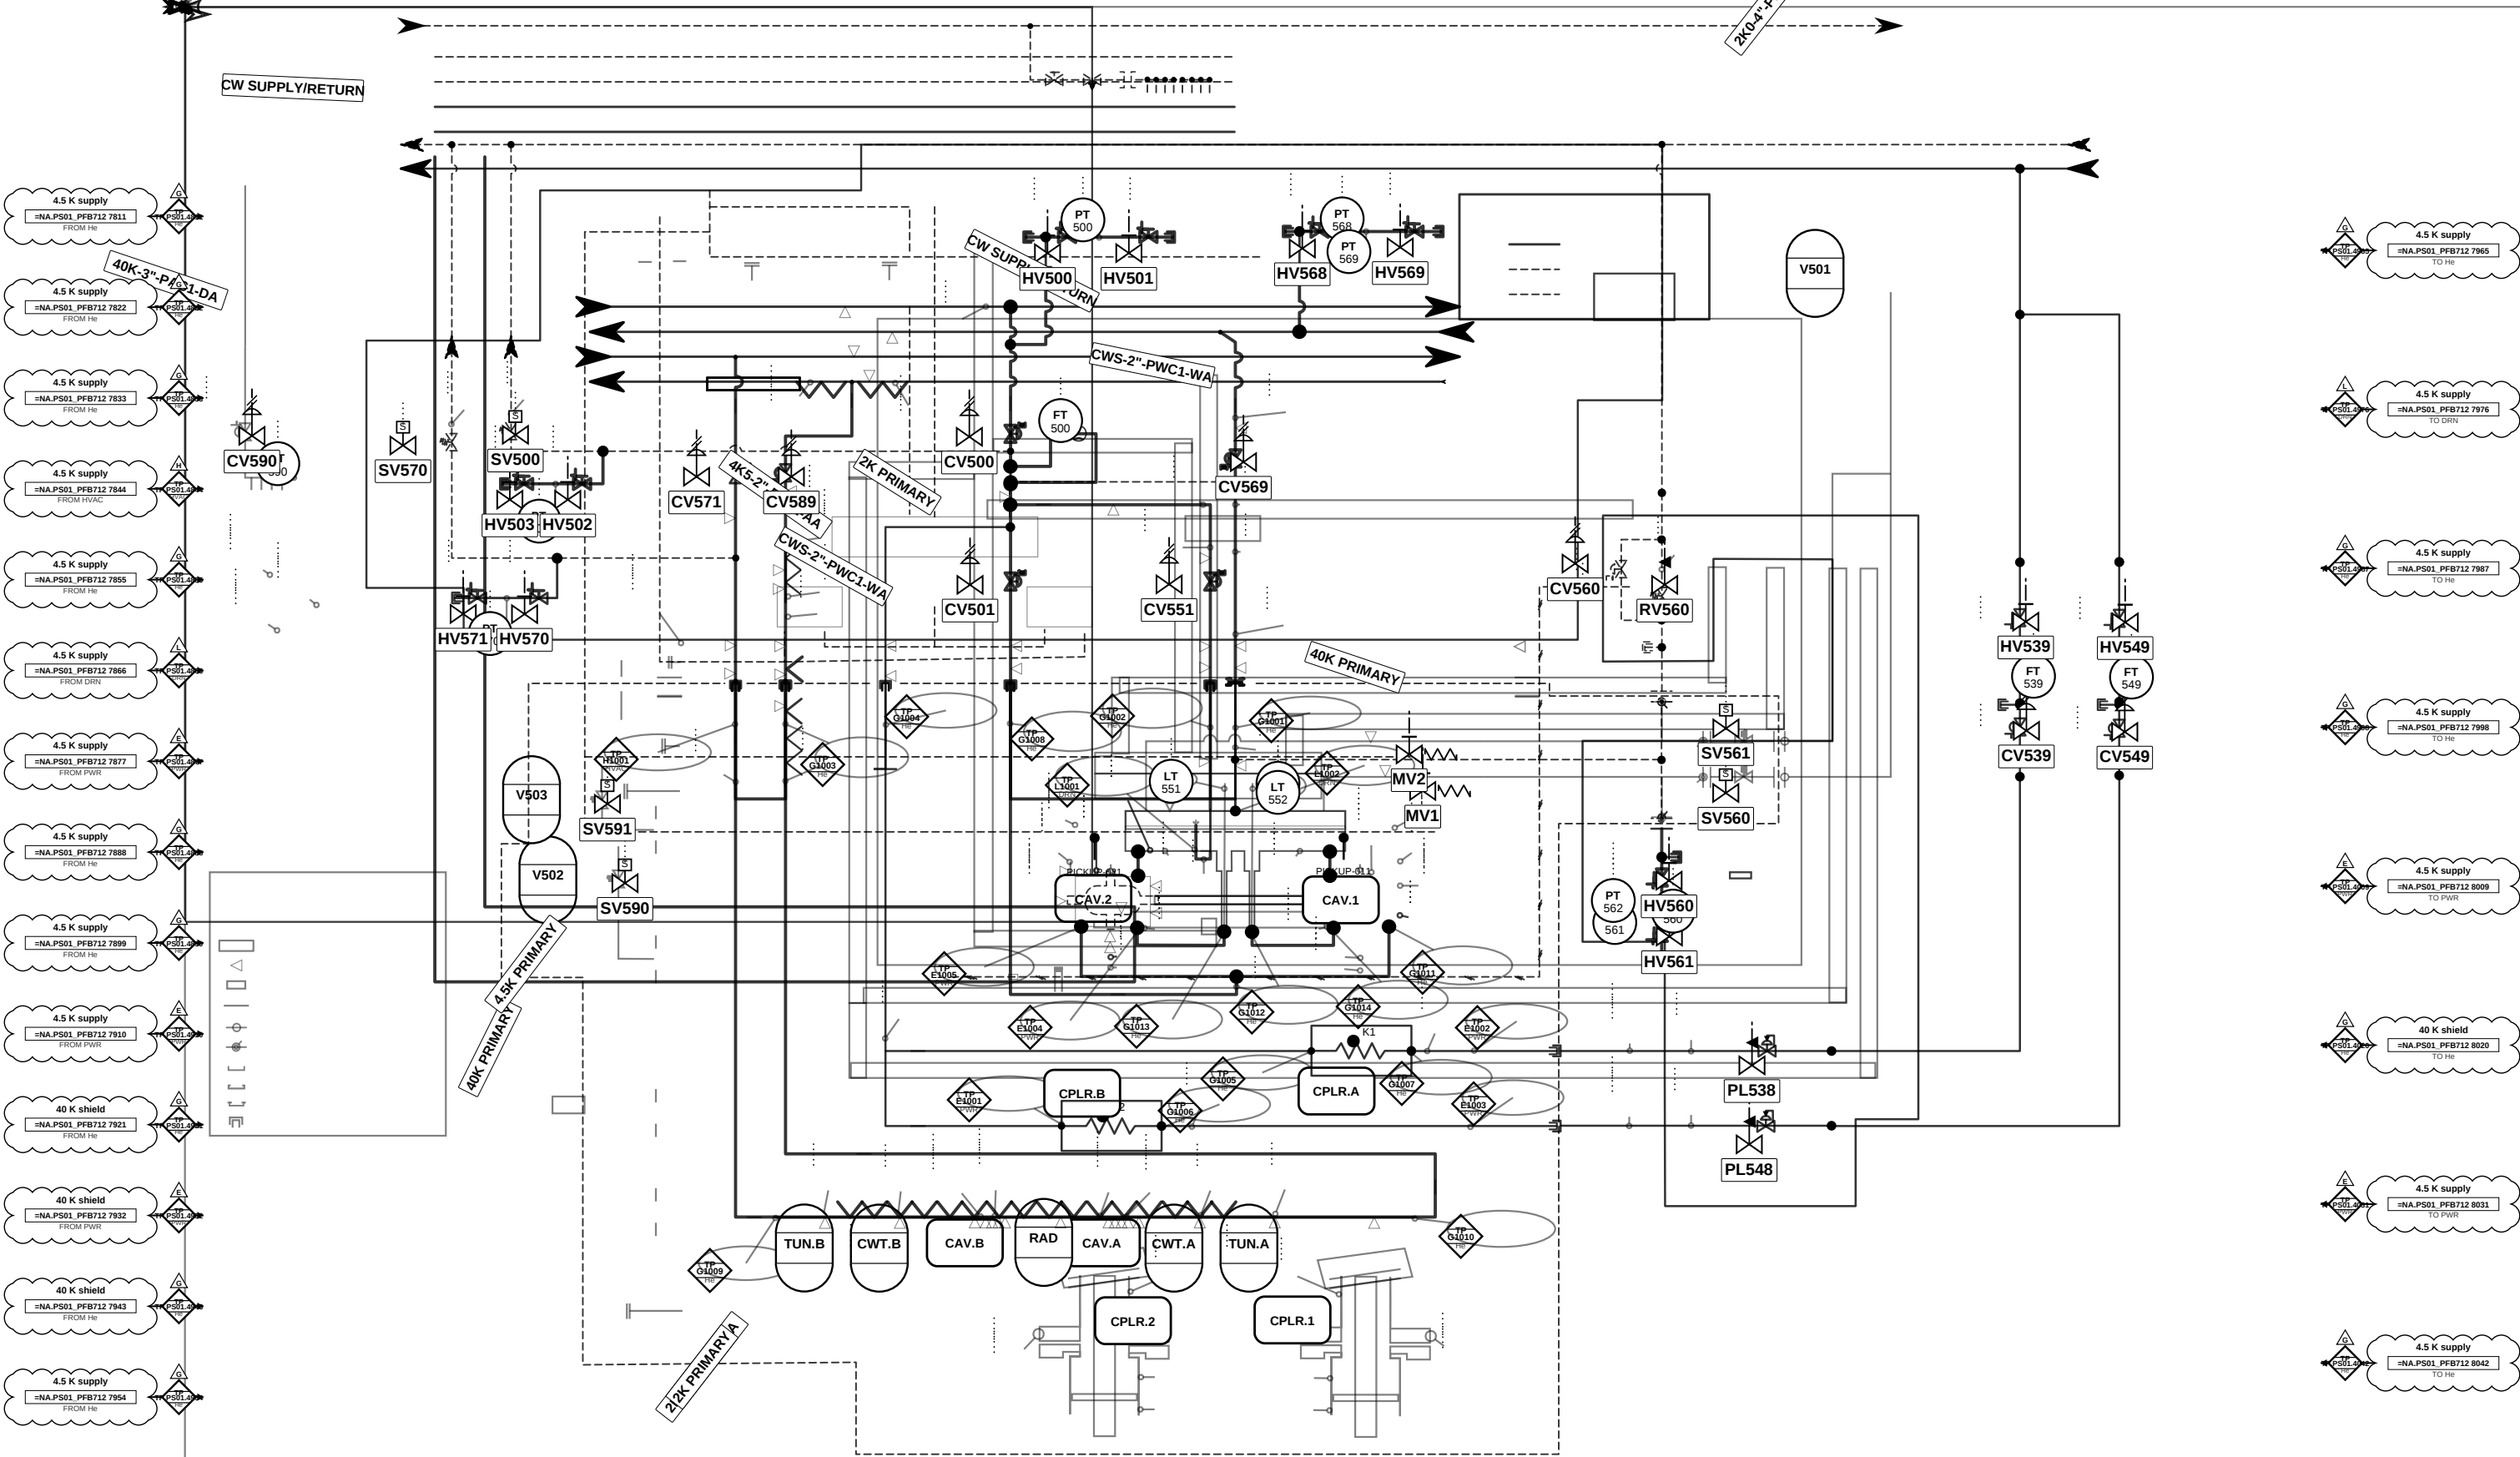

CONSULTANT Mott MacDonald Bristol, UK	CLIENT SCK CEN Boeretang 200, 2400 Mol, BE MYRRHA / MINERVA Phase 1	REVISIONS				App'd	APPROVALS		MINERVA CryoCell - SCK CEN QCELL / LB - Cryogenic Circuits (40 K / 4. DWG No. =NA.PS01_PFB712 MMD Proj. 411066 Scale NTS Suitability S2 - FOR ACCEPTANCE Security RESTRICTED Size / Std A3 / ISO10628 / ISA-5.1 Sheet Sheet1 of 2 - Cryogenic Variant CONTROL-CENTRIC_MONO
		Rev	Date	Description			Designed	QSYS	
		C1	2026-06	v3 refinement - layers/legibil			Drawn	ACR	
		B1	2026-05	v2 split sheets			Checked	ACR	
		A1	2026-04	First issue			Approved	PM	