


P&ID - QCELL / LB - Cryogenic Circuits (40 K / 4.5 K / 2 K + HX)

CONTROL-CENTRIC

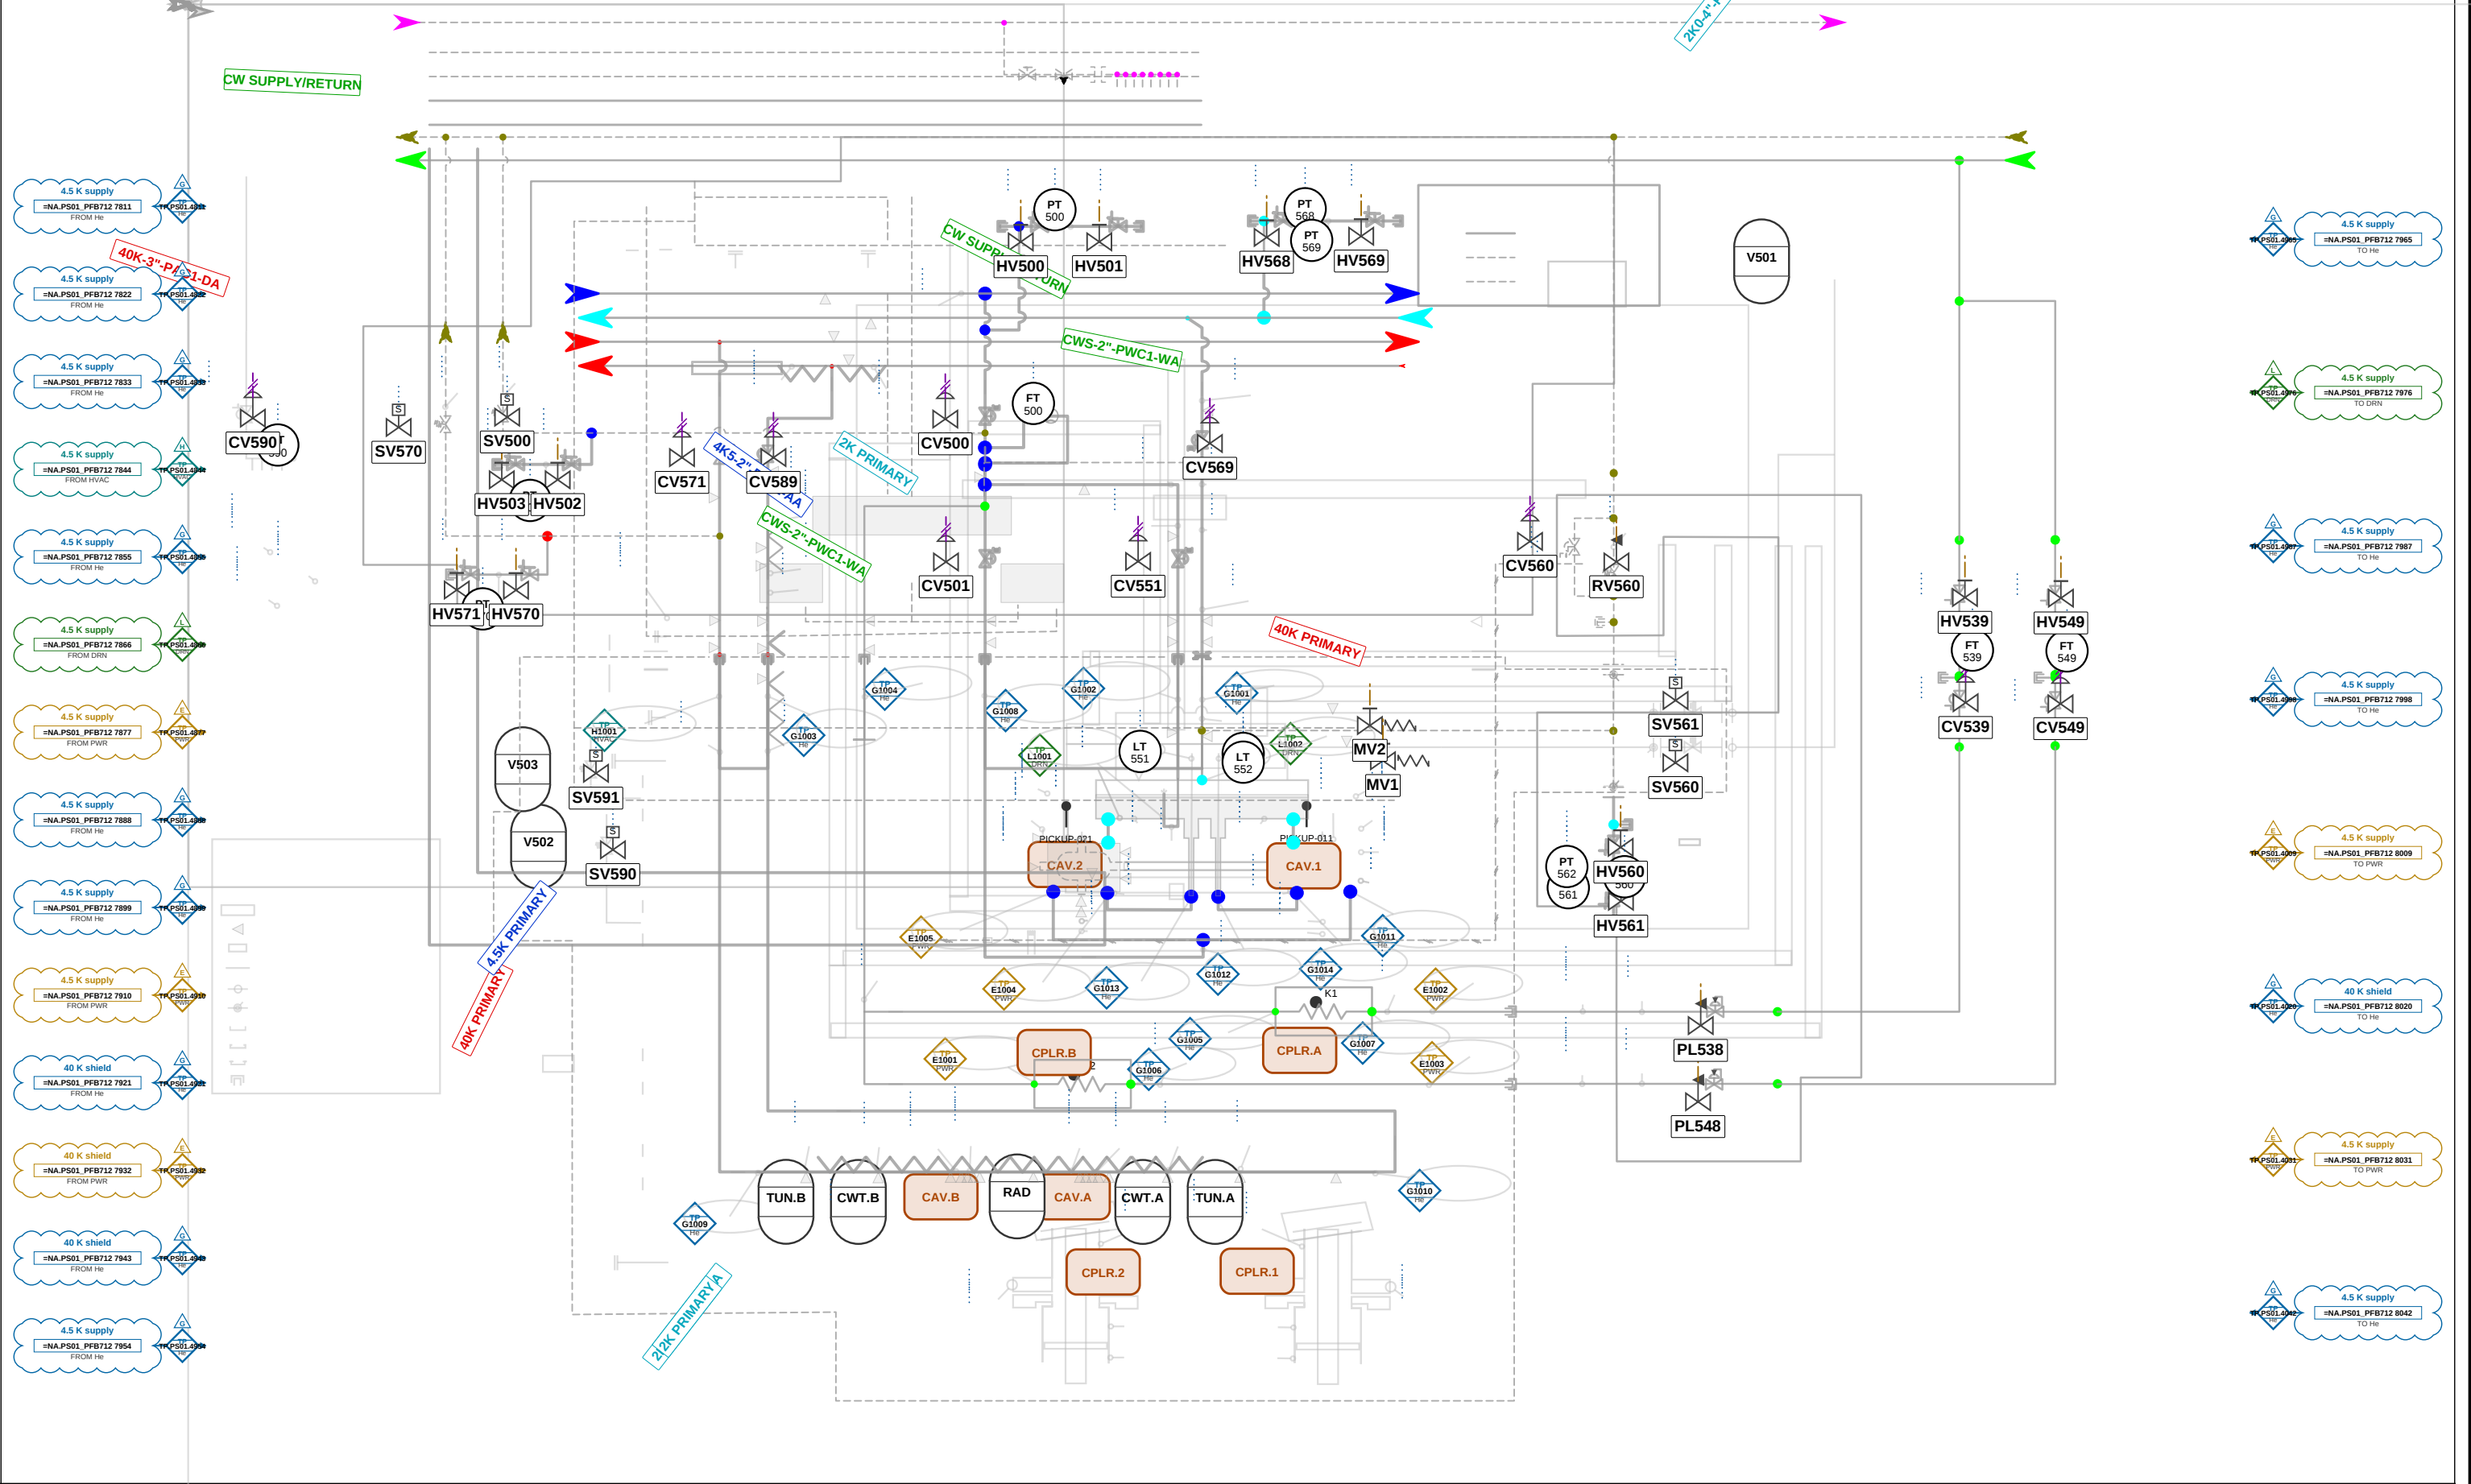

CONSULTANT	CLIENT	REVISIONS	APPROVALS			MINERVA CryoCell - SCK CEN
Mott MacDonald	SCK CEN	RevDateDescriptionApp'd	Designed	QSYS		QCELL / LB - Cryogenic Circuits (40 K / 4.
Bristol, UK	Boeretang 200, 2400 Mol, BE	C12026-06v3 refinement - layers/legibilACR	Drawn	ACR		DWG No. =NA.PS01_PFB712
	MYRRHA / MINERVA Phase 1	B12026-05v2 split sheetsACR	Checked	ACR		MMD Proj. 411066
		A12026-04First issueACR	Approved	PM		Scale NTS
						Suitability S2 - FOR ACCEPTANCE
						Security RESTRICTED
						Size / Std A3 / ISO10628 / ISA-5.1
						Sheet Sheet1 of 2 - Cryogenic
						Variant CONTROL-CENTRIC