


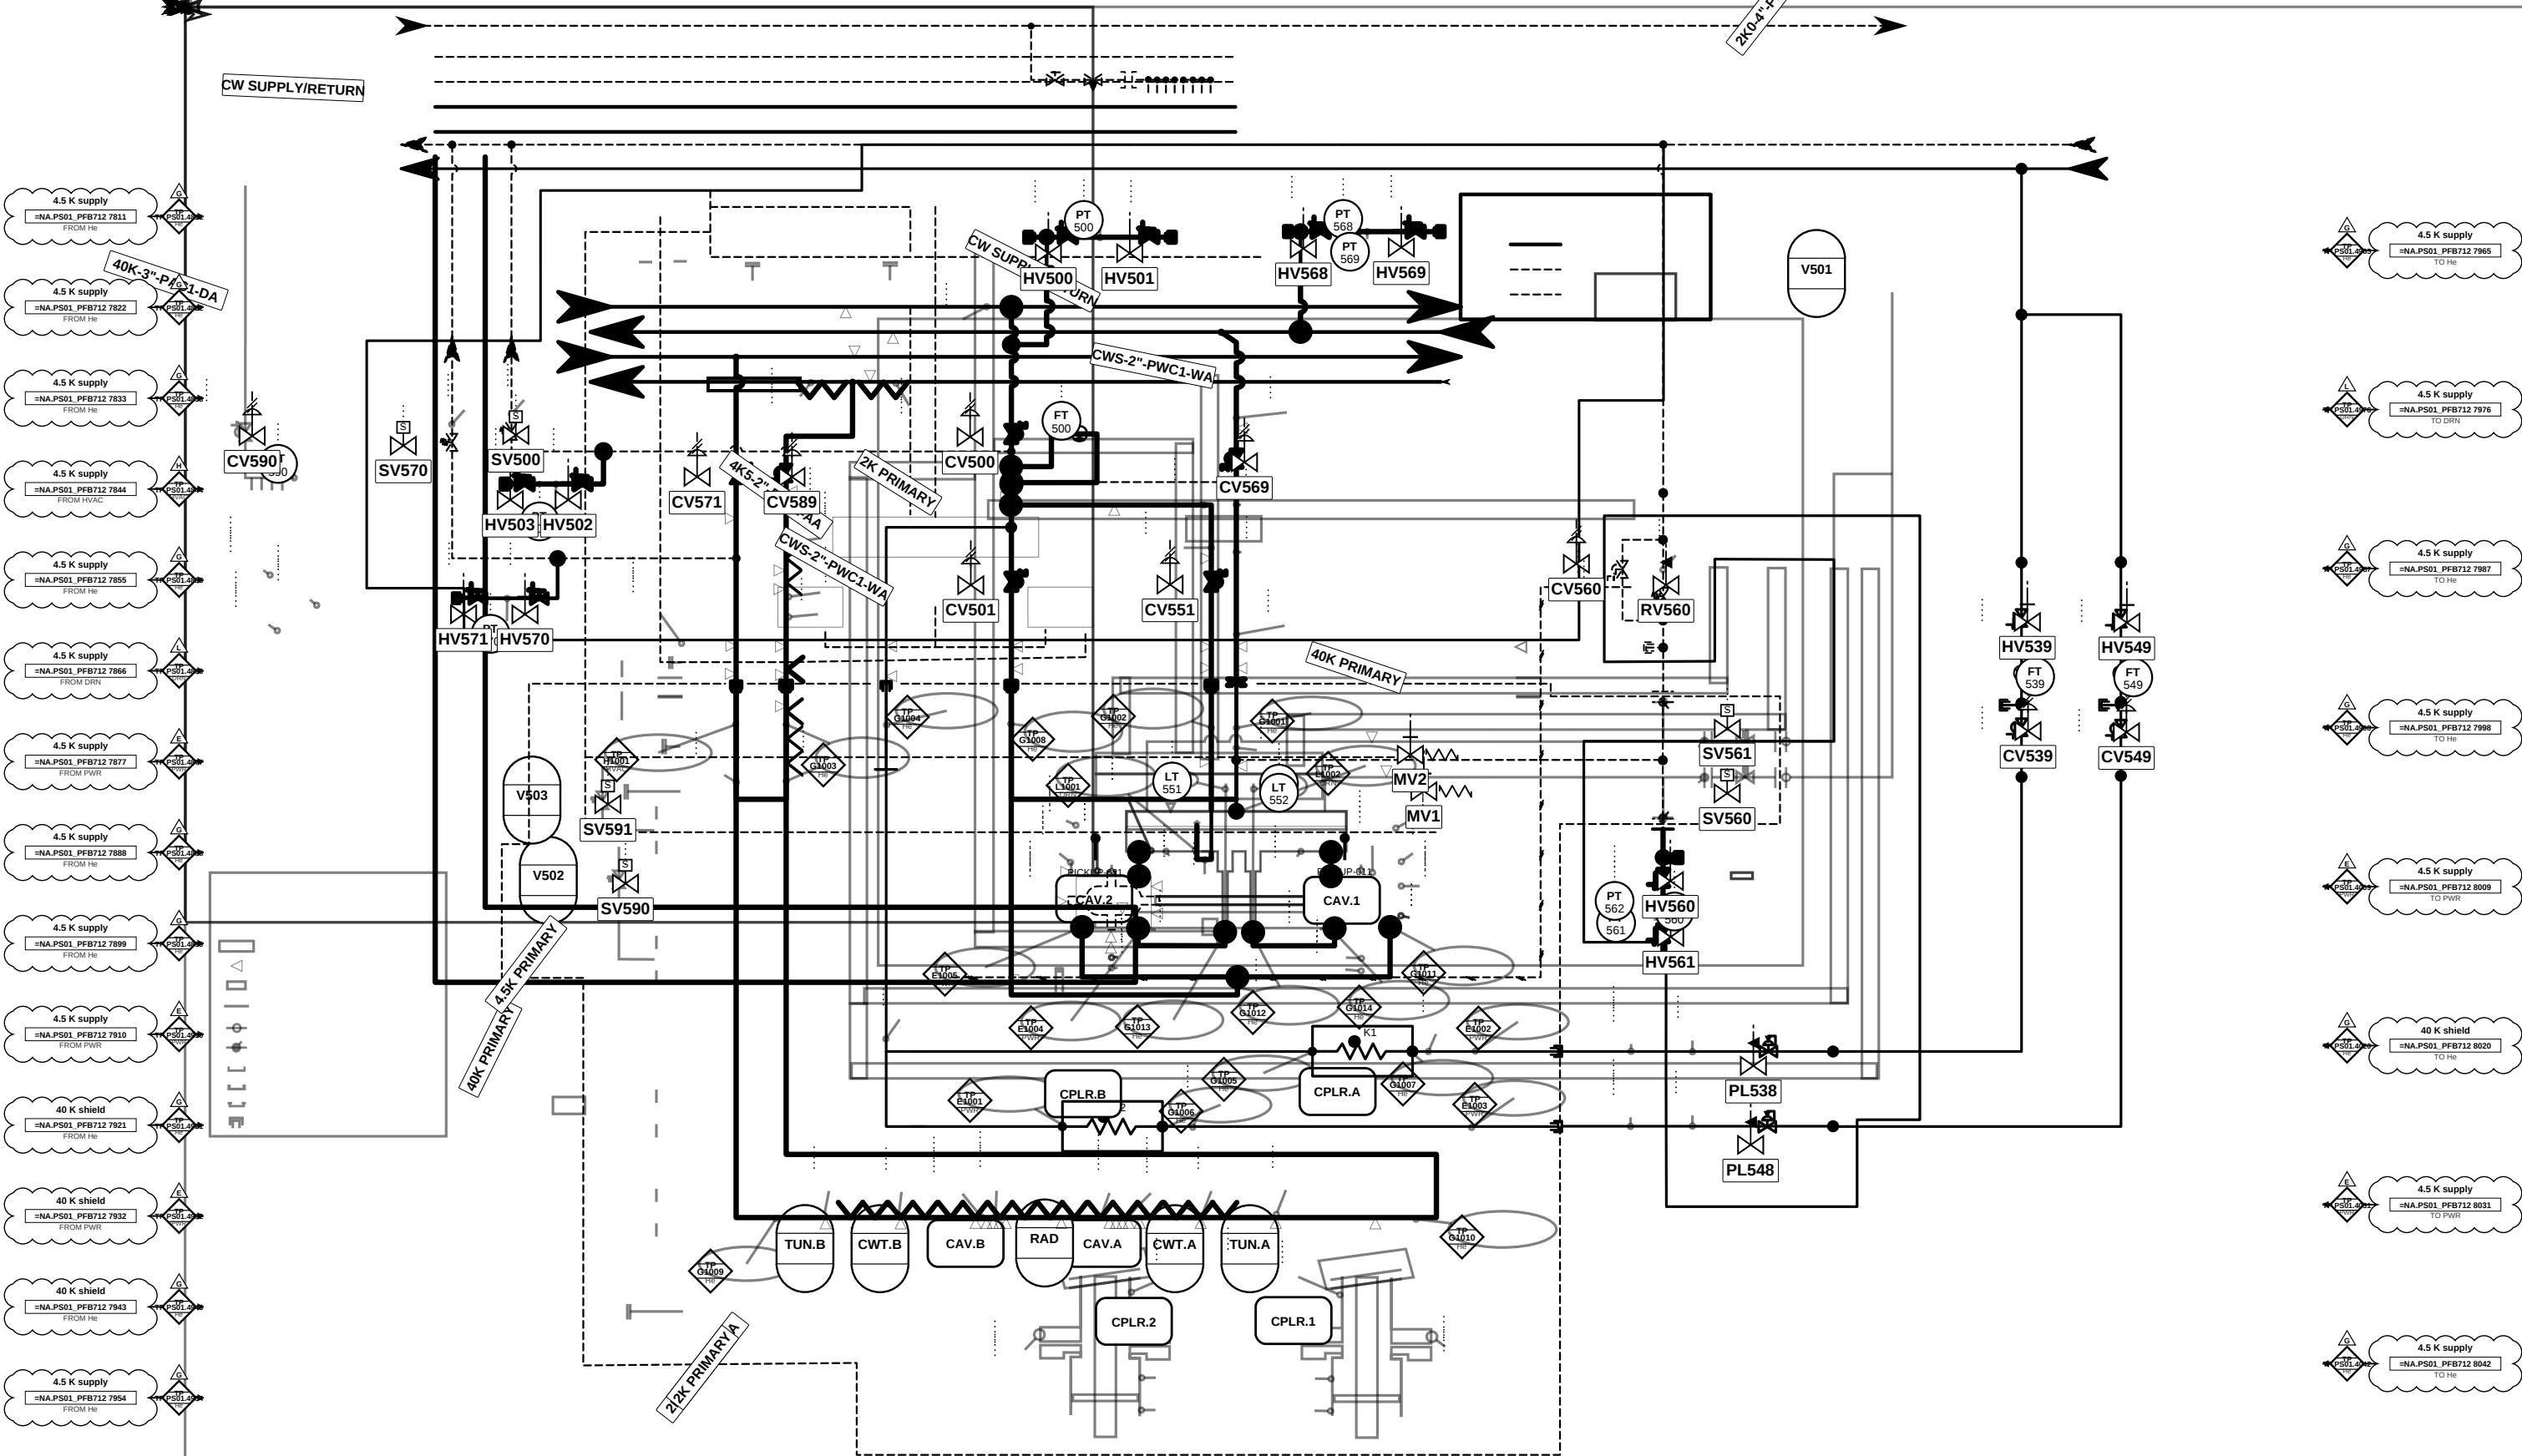

CONSULTANT Mott MacDonald Bristol, UK	CLIENT SCK CEN Boeretang 200, 2400 Mol, BE MYRRHA / MINERVA Phase 1	REVISIONS <table><thead><tr><th>Rev</th><th>Date</th><th>Description</th><th>App'd</th></tr></thead><tbody><tr><td>C1</td><td>2026-06</td><td>v3 refinement - layers/legibil</td><td>ACR</td></tr><tr><td>B1</td><td>2026-05</td><td>v2 split sheets</td><td>ACR</td></tr><tr><td>A1</td><td>2026-04</td><td>First issue</td><td>ACR</td></tr></tbody></table>			Rev	Date	Description	App'd	C1	2026-06	v3 refinement - layers/legibil	ACR	B1	2026-05	v2 split sheets	ACR	A1	2026-04	First issue	ACR	APPROVALS <table><tbody><tr><td>Designed</td><td>QSYS</td></tr><tr><td>Drawn</td><td>ACR</td></tr><tr><td>Checked</td><td>ACR</td></tr><tr><td>Approved</td><td>PM</td></tr></tbody></table>		Designed	QSYS	Drawn	ACR	Checked	ACR	Approved	PM	MINERVA CryoCell - SCK CEN QCELL / LB - Cryogenic Circuits (40 K / 4. DWG No. NA.PS01_PFB712 MMD Proj. 411066 Scale NTS Suitability S2 - FOR ACCEPTANCE Security RESTRICTED Size / Std A3 / ISO10628 / ISA-5.1 Sheet Sheet1 of 2 - Cryogenic Variant STANDARD_MONO
		Rev	Date	Description	App'd																										
		C1	2026-06	v3 refinement - layers/legibil	ACR																										
		B1	2026-05	v2 split sheets	ACR																										
		A1	2026-04	First issue	ACR																										
Designed	QSYS																														
Drawn	ACR																														
Checked	ACR																														
Approved	PM																														