


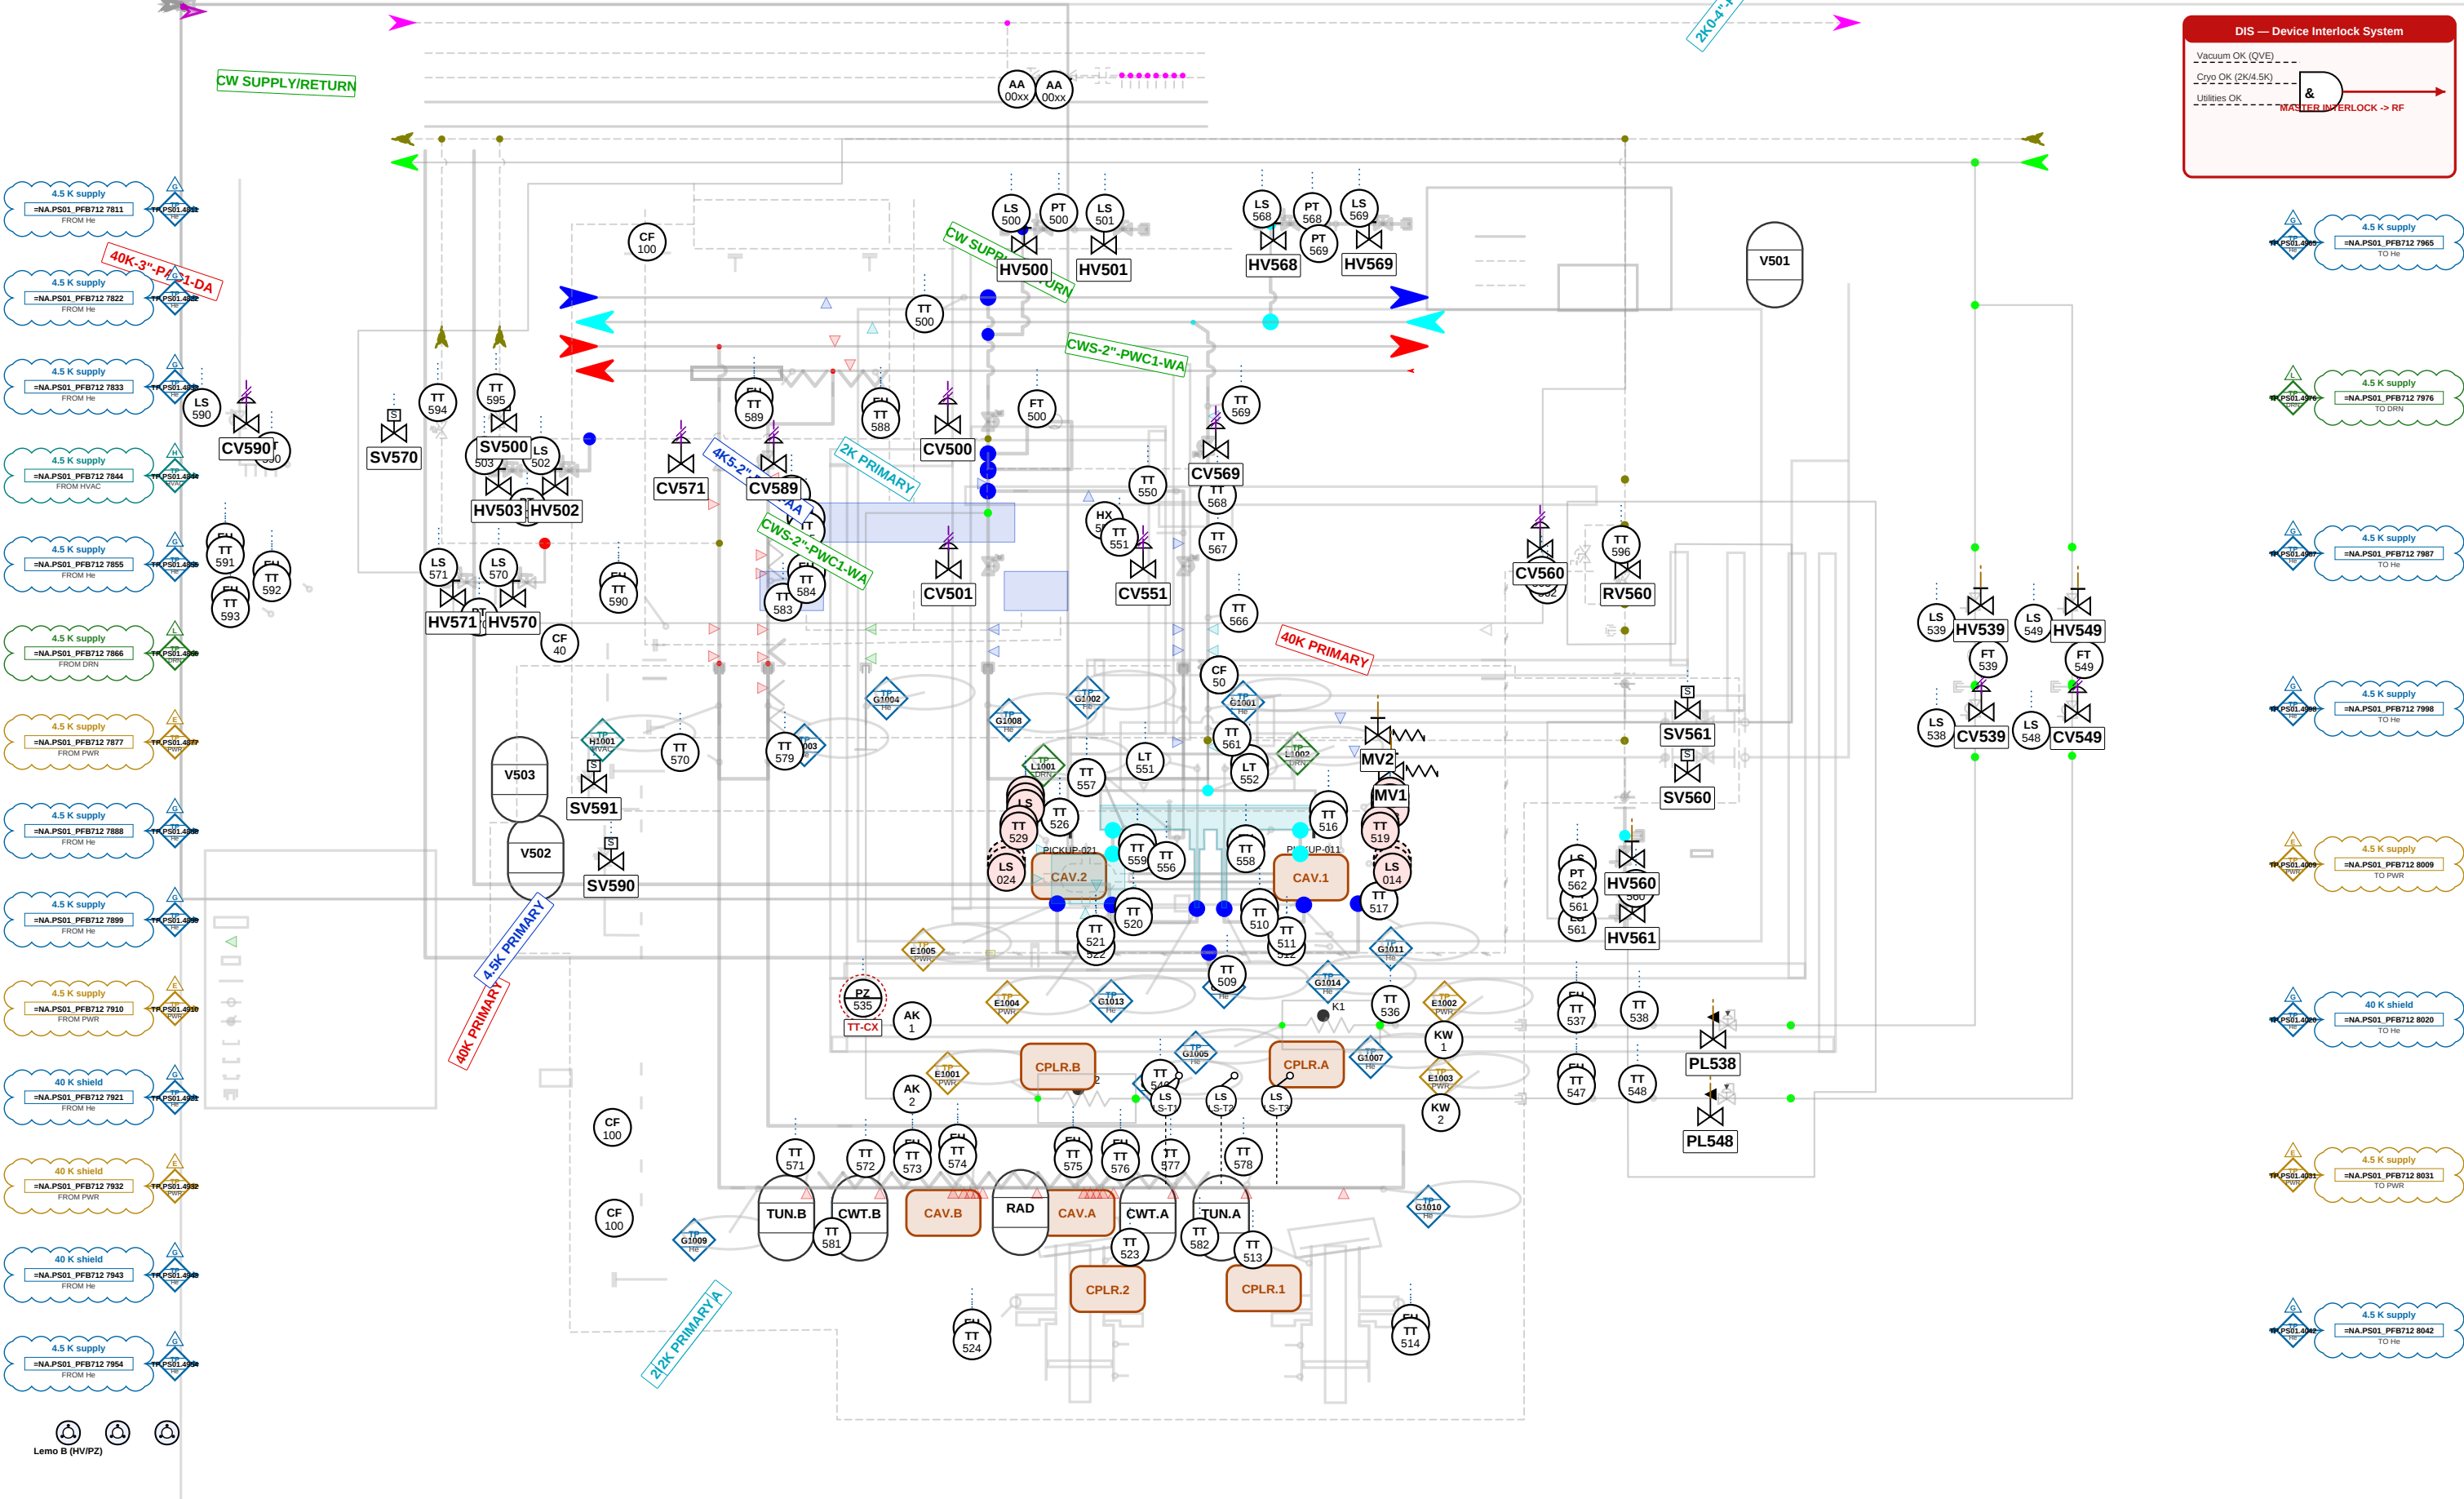

CONSULTANT Mott MacDonald Bristol, UK	CLIENT SCK CEN Boeretang 200, 2400 Mol, BE MYRRHA / MINERVA Phase 1	REVISIONS		Description	App'd	APPROVALS		MINERVA CryoCell - SCK CEN QCELL / LB - Instrumentation & Control DWG No. =NA.PS01_PFB712 MMD Proj. 411066 Scale NTS Suitability S2 - FOR ACCEPTANCE Security RESTRICTED Size / Std A3 / ISO10628 / ISA-5.1 Sheet Sheet2 of 2 - Instrumentation Variant STANDARD
		Rev	Date			Designed	QSYS	
		C1	2026-06			Drawn	ACR	
		B1	2026-05			Checked	ACR	
		A1	2026-04			Approved	PM	