


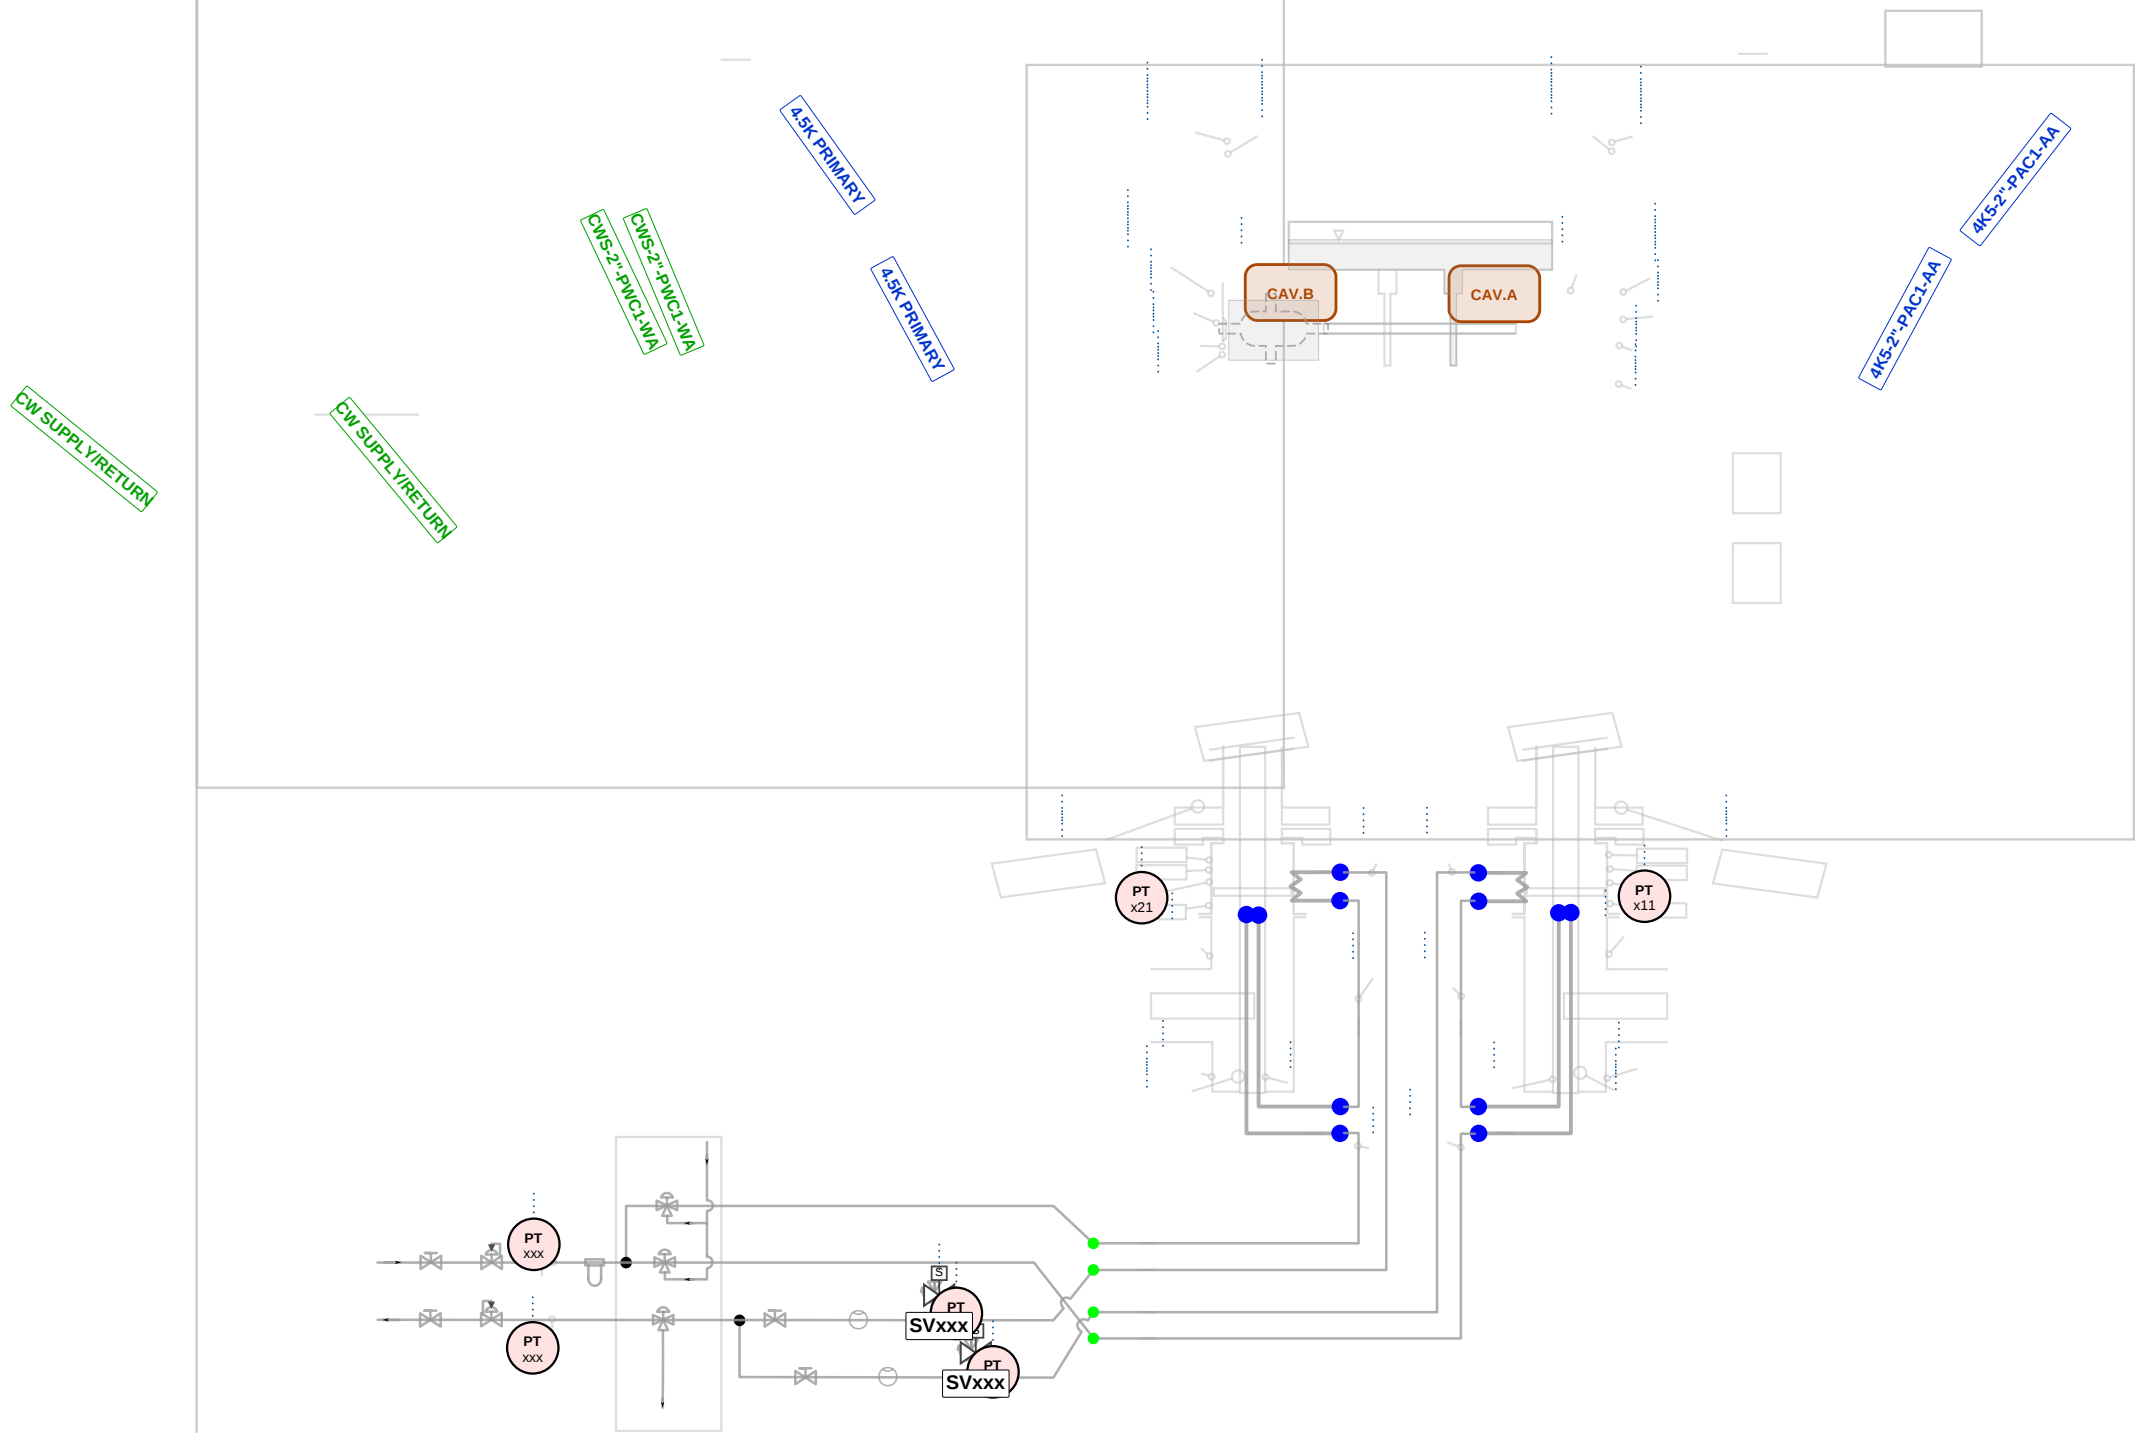

CONSULTANT Mott MacDonald Bristol, UK		CLIENT SCK CEN Boeretang 200, 2400 Mol, BE MYRRHA / MINERVA Phase 1	REVISIONS			App'd	APPROVALS		MINERVA CryoCell - SCK CEN RFCELL (seen by ACR) - Process Flow (DI-Wa DWG No. =NA.PS01_PFB713 MMD Proj. 411066 Scale NTS Suitability S2 - FOR ACCEPTANCE Security RESTRICTED Size / Std A3 / ISO10628 / ISA-5.1 Sheet Sheet1 of 2 - Process Variant CONTROL-CENTRIC
			Rev	Date	Description		Designed	QSYS	
			C1	2026-06	v3 refinement - layers/legibil		Drawn	ACR	
			B1	2026-05	v2 split sheets		Checked	ACR	
			A1	2026-04	First issue		Approved	PM	