


P&ID - QCELL / LB - Instrumentation & Control

CONTROL-CENTRIC

COLD HEADER - Line A (4.5 K) / Line B (2 K)

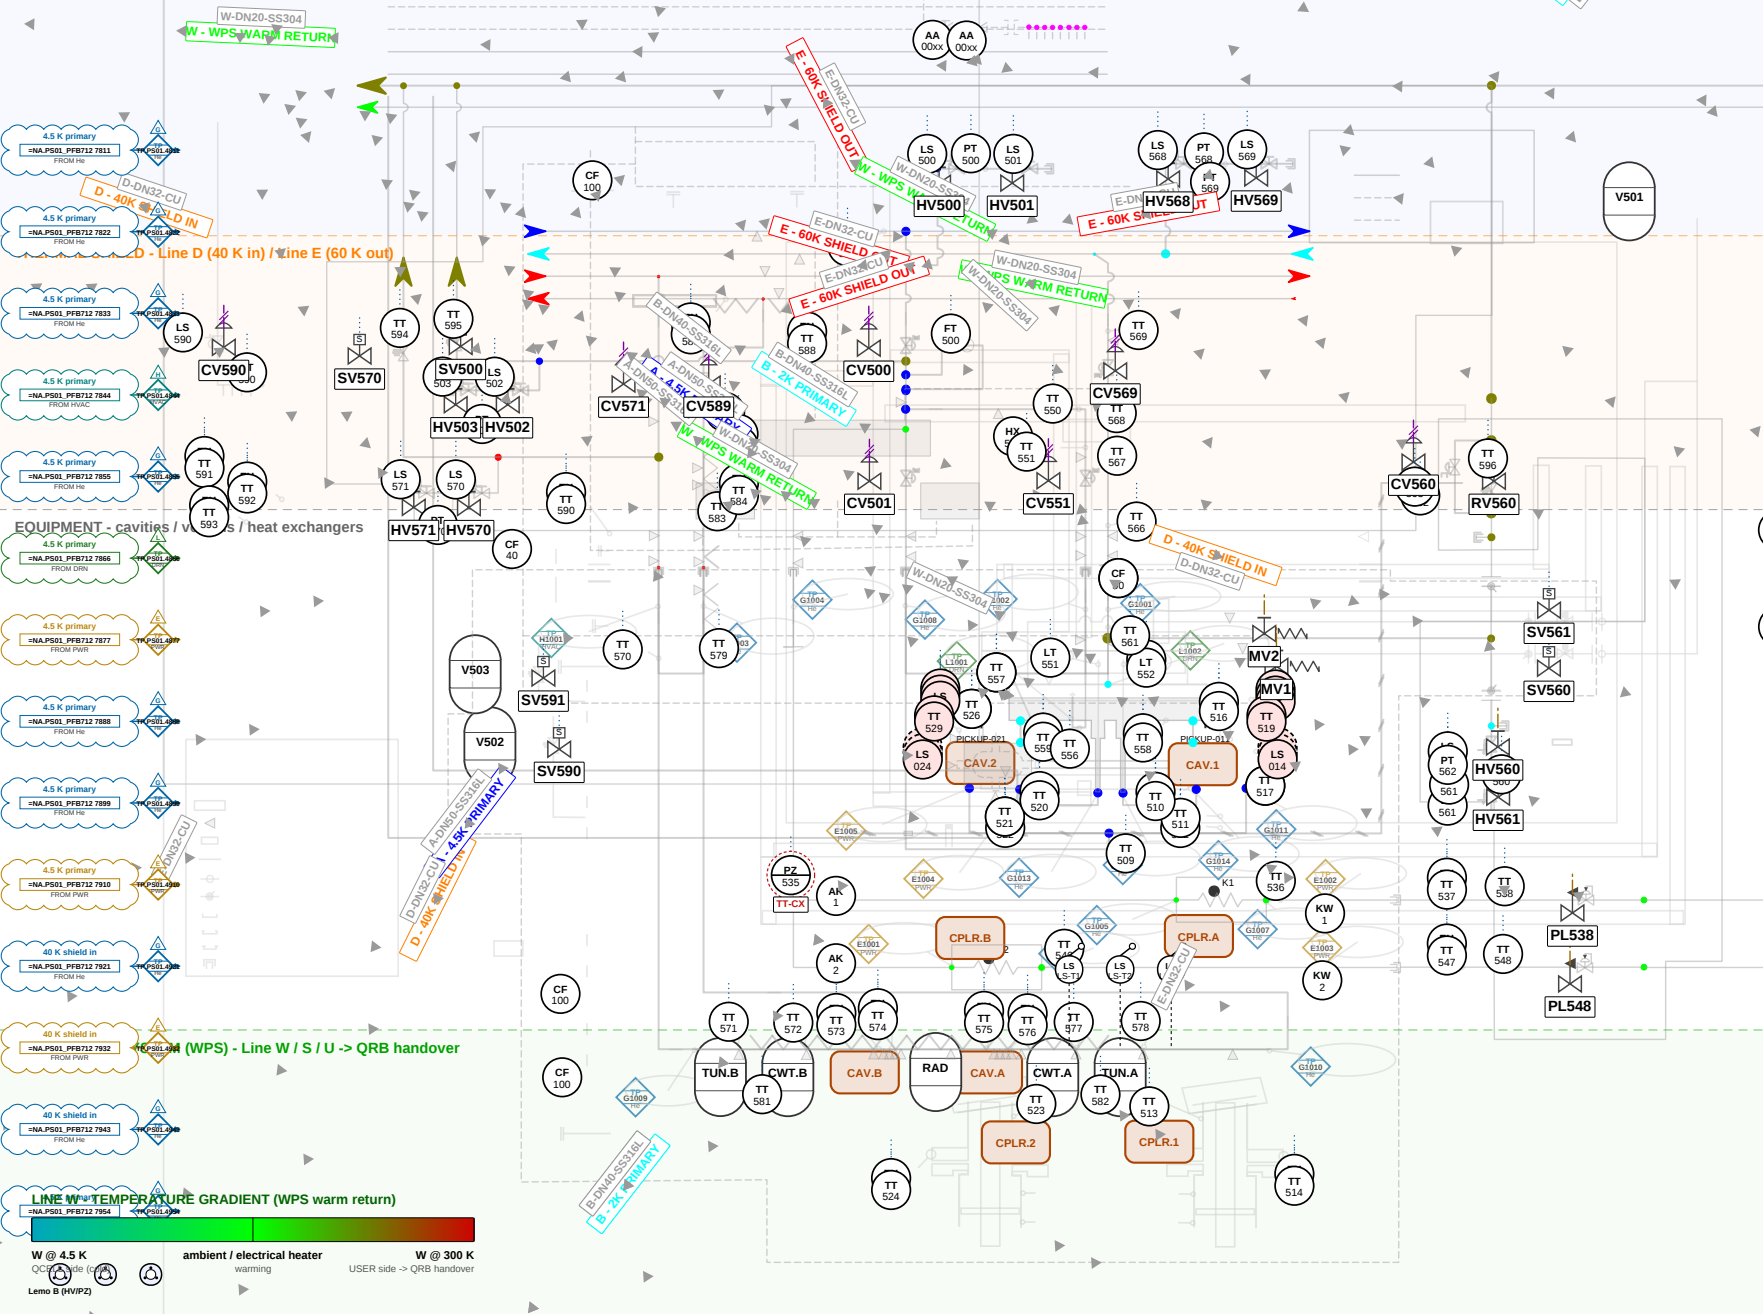

INTERACTIVE LEGEND
toggle: layer "3d_Legend_INTERACTIVE"

LINE SPECIFICATION TABLE

LINE	TEMP	PRESS	DN	MOC
COLD-HEADER				
A	4.5 K	3 bar	DN50	SS316L
A'	4.5 K	3 bar	DN105	SS316L
B	2 K	27 mbar	DN40	SS316L
B'	2 K	27 mbar	DN105	SS316L
THERMAL SHIELD				
D	40 K	14 bar	DN32	CU
D'	40 K	14 bar	DN100	CU
E	60 K	13 bar	DN32	CU
E'	60 K	13 bar	DN100	CU
WARM (WPS)				
W	4.5 K-300	6 bar	DN10	SS304
S	2-292 K	1.05 bar	DN15	SS304
U	292 K	14 bar	DN15	SS304
REFERENCE				
OS				

SIGNAL TYPES (0.25 mm)

- Pneumatic (dash + //)
- Electric (dotted)
- Hydraulic (dash-dot)

INSTRUMENTS / SCOPE

- Field instrument (white box tag)
- Panel / safety (line)
- TP scope diamond (edge = TP layer)

Car: B=Building, C=Chemical, E=Electrical, G=Compressed gases
H=HVAC, L=Liquid waste, S=Solid waste, W=Water

CONSULTANT Mott MacDonald Bristol, UK	CLIENT SCK CEN Boeing 200, 2400 Mbl, BE MYRRHA / MINERVA Phase 1	REVISIONS Rev	Date	Description	App'd	APPROVALS Designed QSYS Drawn ACR Checked ACR Approved PM	MINERVA CryoCell - SCK CEN QCELL / LB - Instrumentation & Control DWG No: -NA.P501.PF8712 MMD Proj: 411966 Scale: NTS Suitability: S2 - FOR ACCEPTANCE Security: RESTRICTED Size / Std: A3 / ISO1628 / ISA-5.1 Sheet: Sheet 2 of 2 - Instrumentation Variant: CONTROL-CENTRIC
			C1	2026-06	v3 refinement - layers/legal	ACR	
			B1	2026-05	v2 split sheets	ACR	
			A1	2026-04	First issue	ACR	