
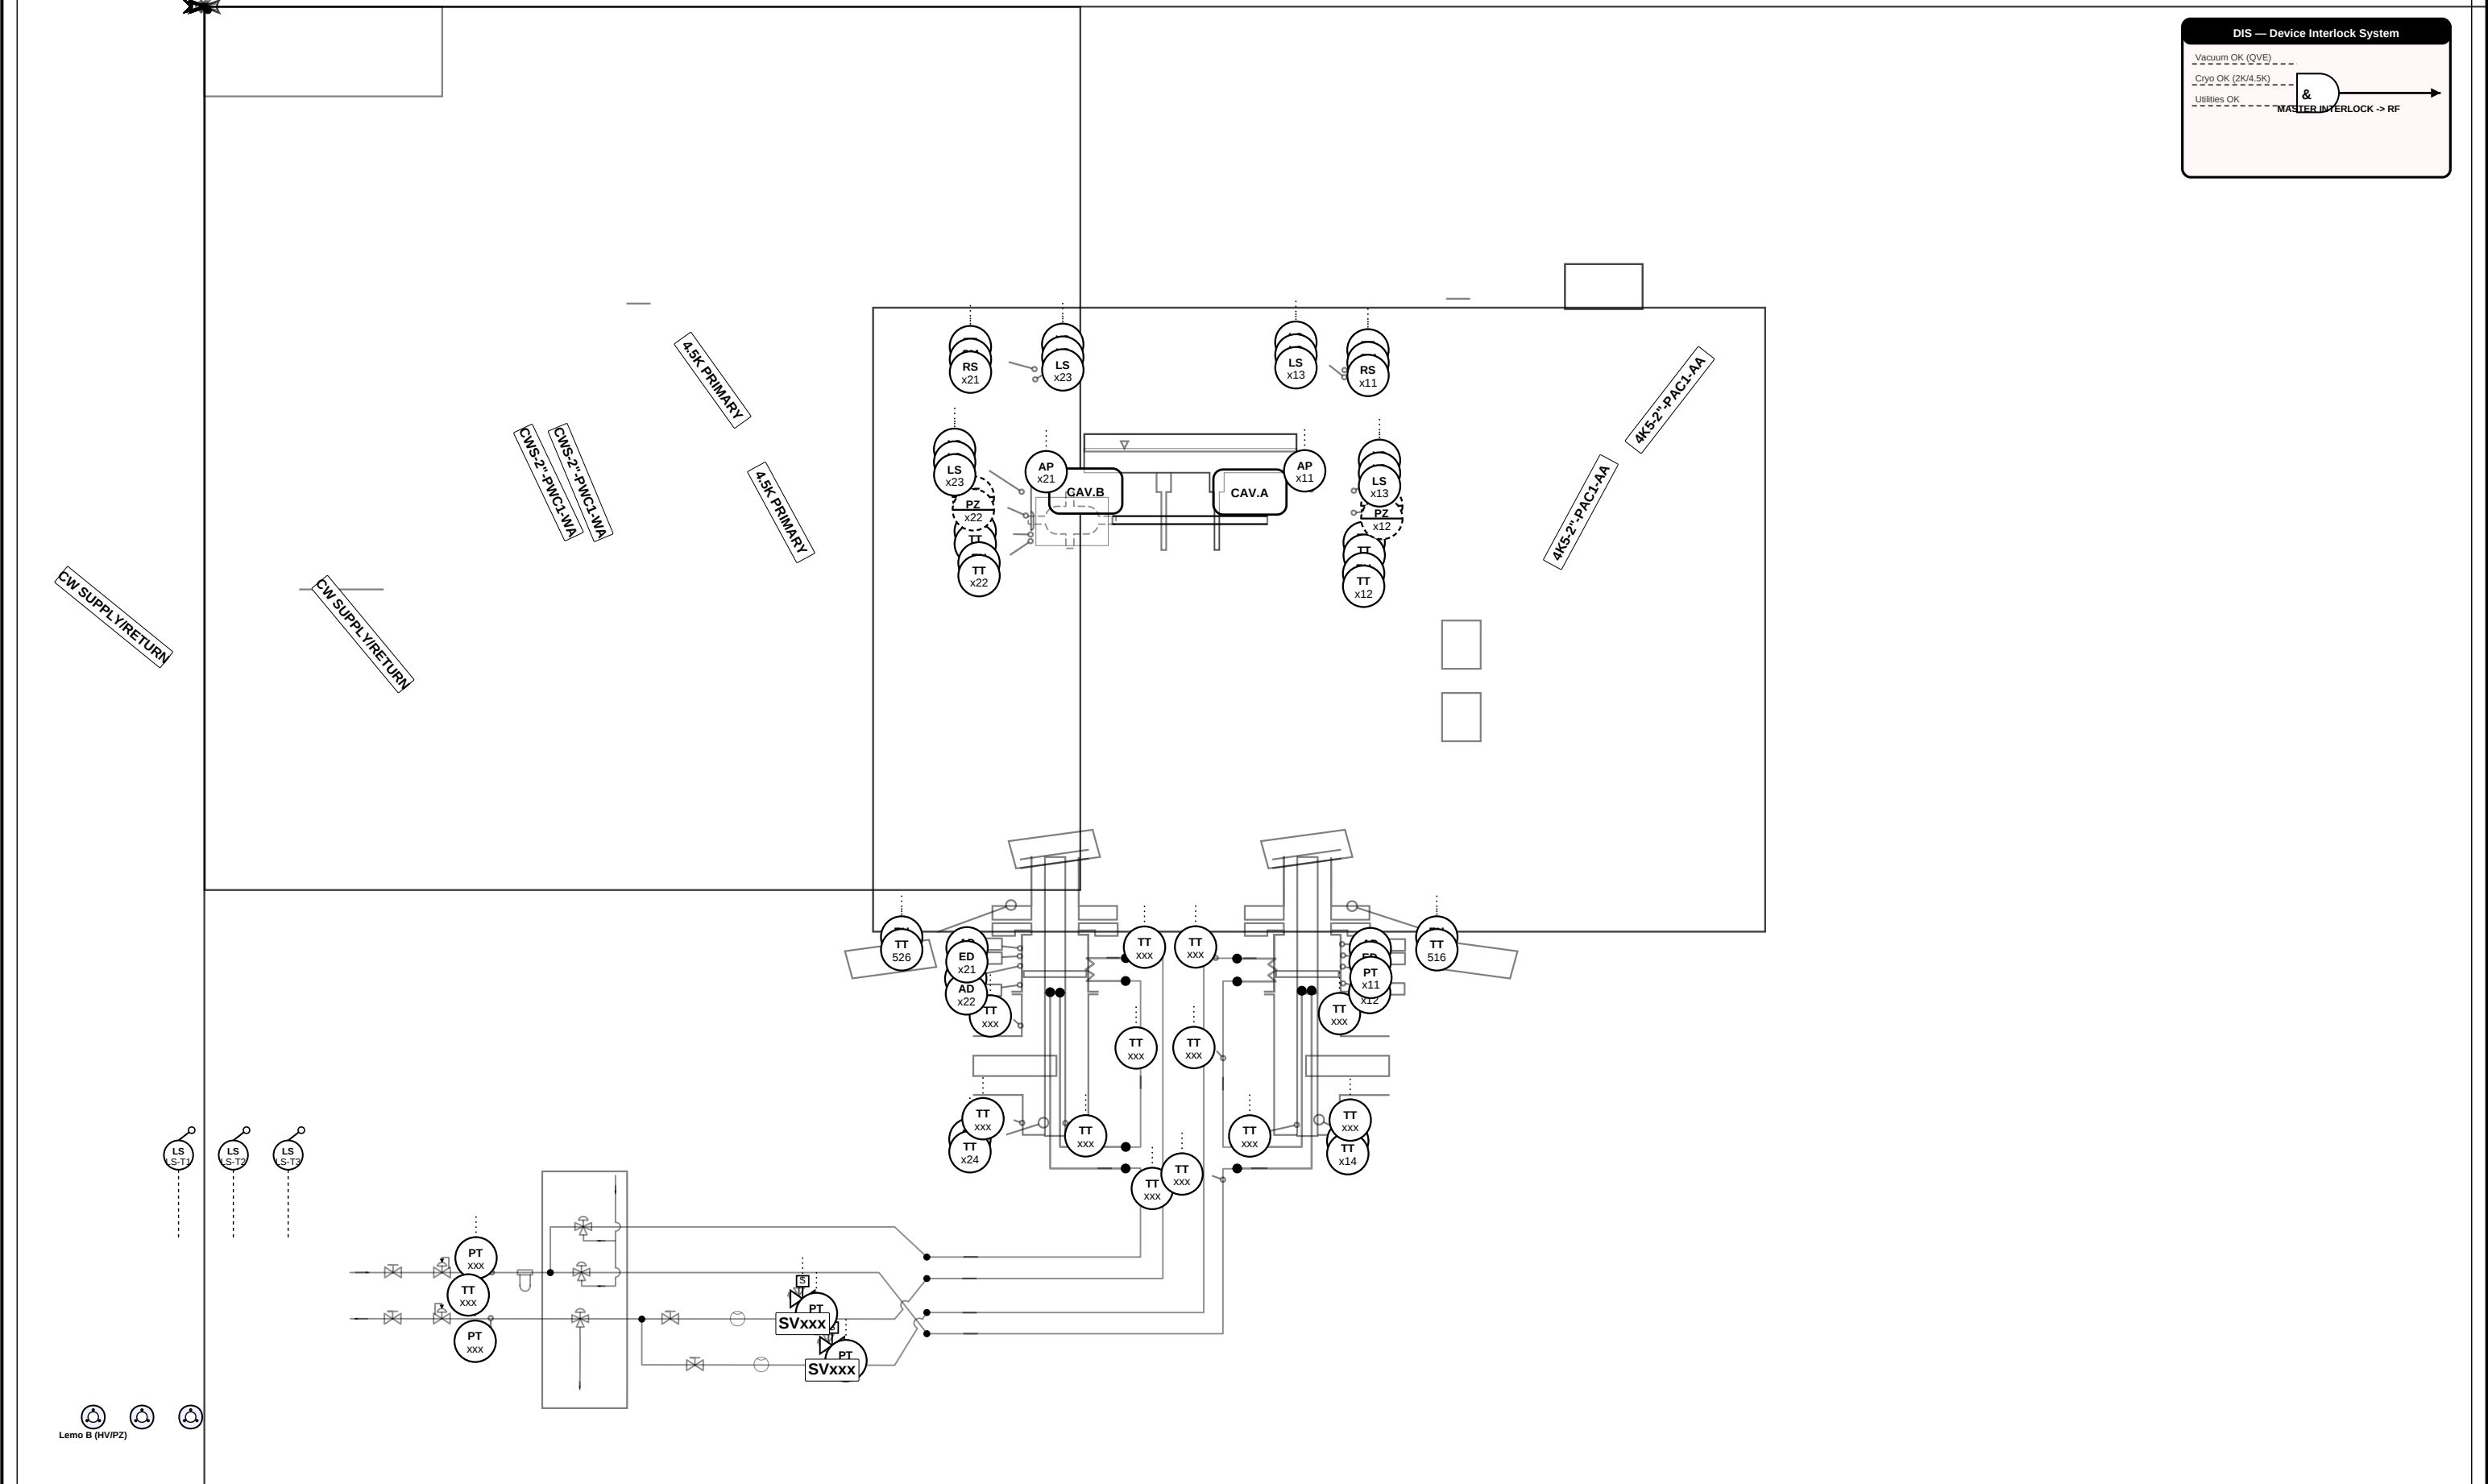


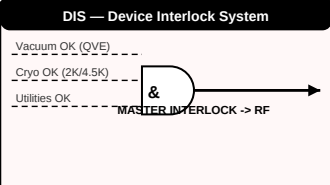

CONSULTANT Mott MacDonald Bristol, UK	CLIENT SCK CEN Boeretang 200, 2400 Mol, BE MYRRHA / MINERVA Phase 1	REVISIONS <table><tr><th>Rev</th><th>Date</th><th>Description</th><th>App'd</th></tr><tr><td>C1</td><td>2026-06</td><td>v3 refinement - layers/legibil</td><td>ACR</td></tr><tr><td>B1</td><td>2026-05</td><td>v2 split sheets</td><td>ACR</td></tr><tr><td>A1</td><td>2026-04</td><td>First issue</td><td>ACR</td></tr></table>	Rev	Date	Description	App'd	C1	2026-06	v3 refinement - layers/legibil	ACR	B1	2026-05	v2 split sheets	ACR	A1	2026-04	First issue	ACR	APPROVALS <table><tr><td>Designed</td><td>QSYS</td></tr><tr><td>Drawn</td><td>ACR</td></tr><tr><td>Checked</td><td>ACR</td></tr><tr><td>Approved</td><td>PM</td></tr></table>	Designed	QSYS	Drawn	ACR	Checked	ACR	Approved	PM	MINERVA CryoCell - SCK CEN RFCELL (seen by ACR) - Instrumentation & C DWG No. = NA.PS01_PFB713 MMD Proj. 411066 Scale NTS Suitability S2 - FOR ACCEPTANCE Security RESTRICTED Size / Std A3 / ISO10628 / ISA-5.1 Sheet Sheet2 of 2 - Instrumentation Variant CONTROL-CENTRIC_MONO
Rev	Date	Description	App'd																									
C1	2026-06	v3 refinement - layers/legibil	ACR																									
B1	2026-05	v2 split sheets	ACR																									
A1	2026-04	First issue	ACR																									
Designed	QSYS																											
Drawn	ACR																											
Checked	ACR																											
Approved	PM																											