


Liquid buffer: 7 L min
Vapour buffer: 5 L min

Diamonds (TP / cat / next) mark the 'last-meter' hand-over between in-scope and out-of-scope assets.

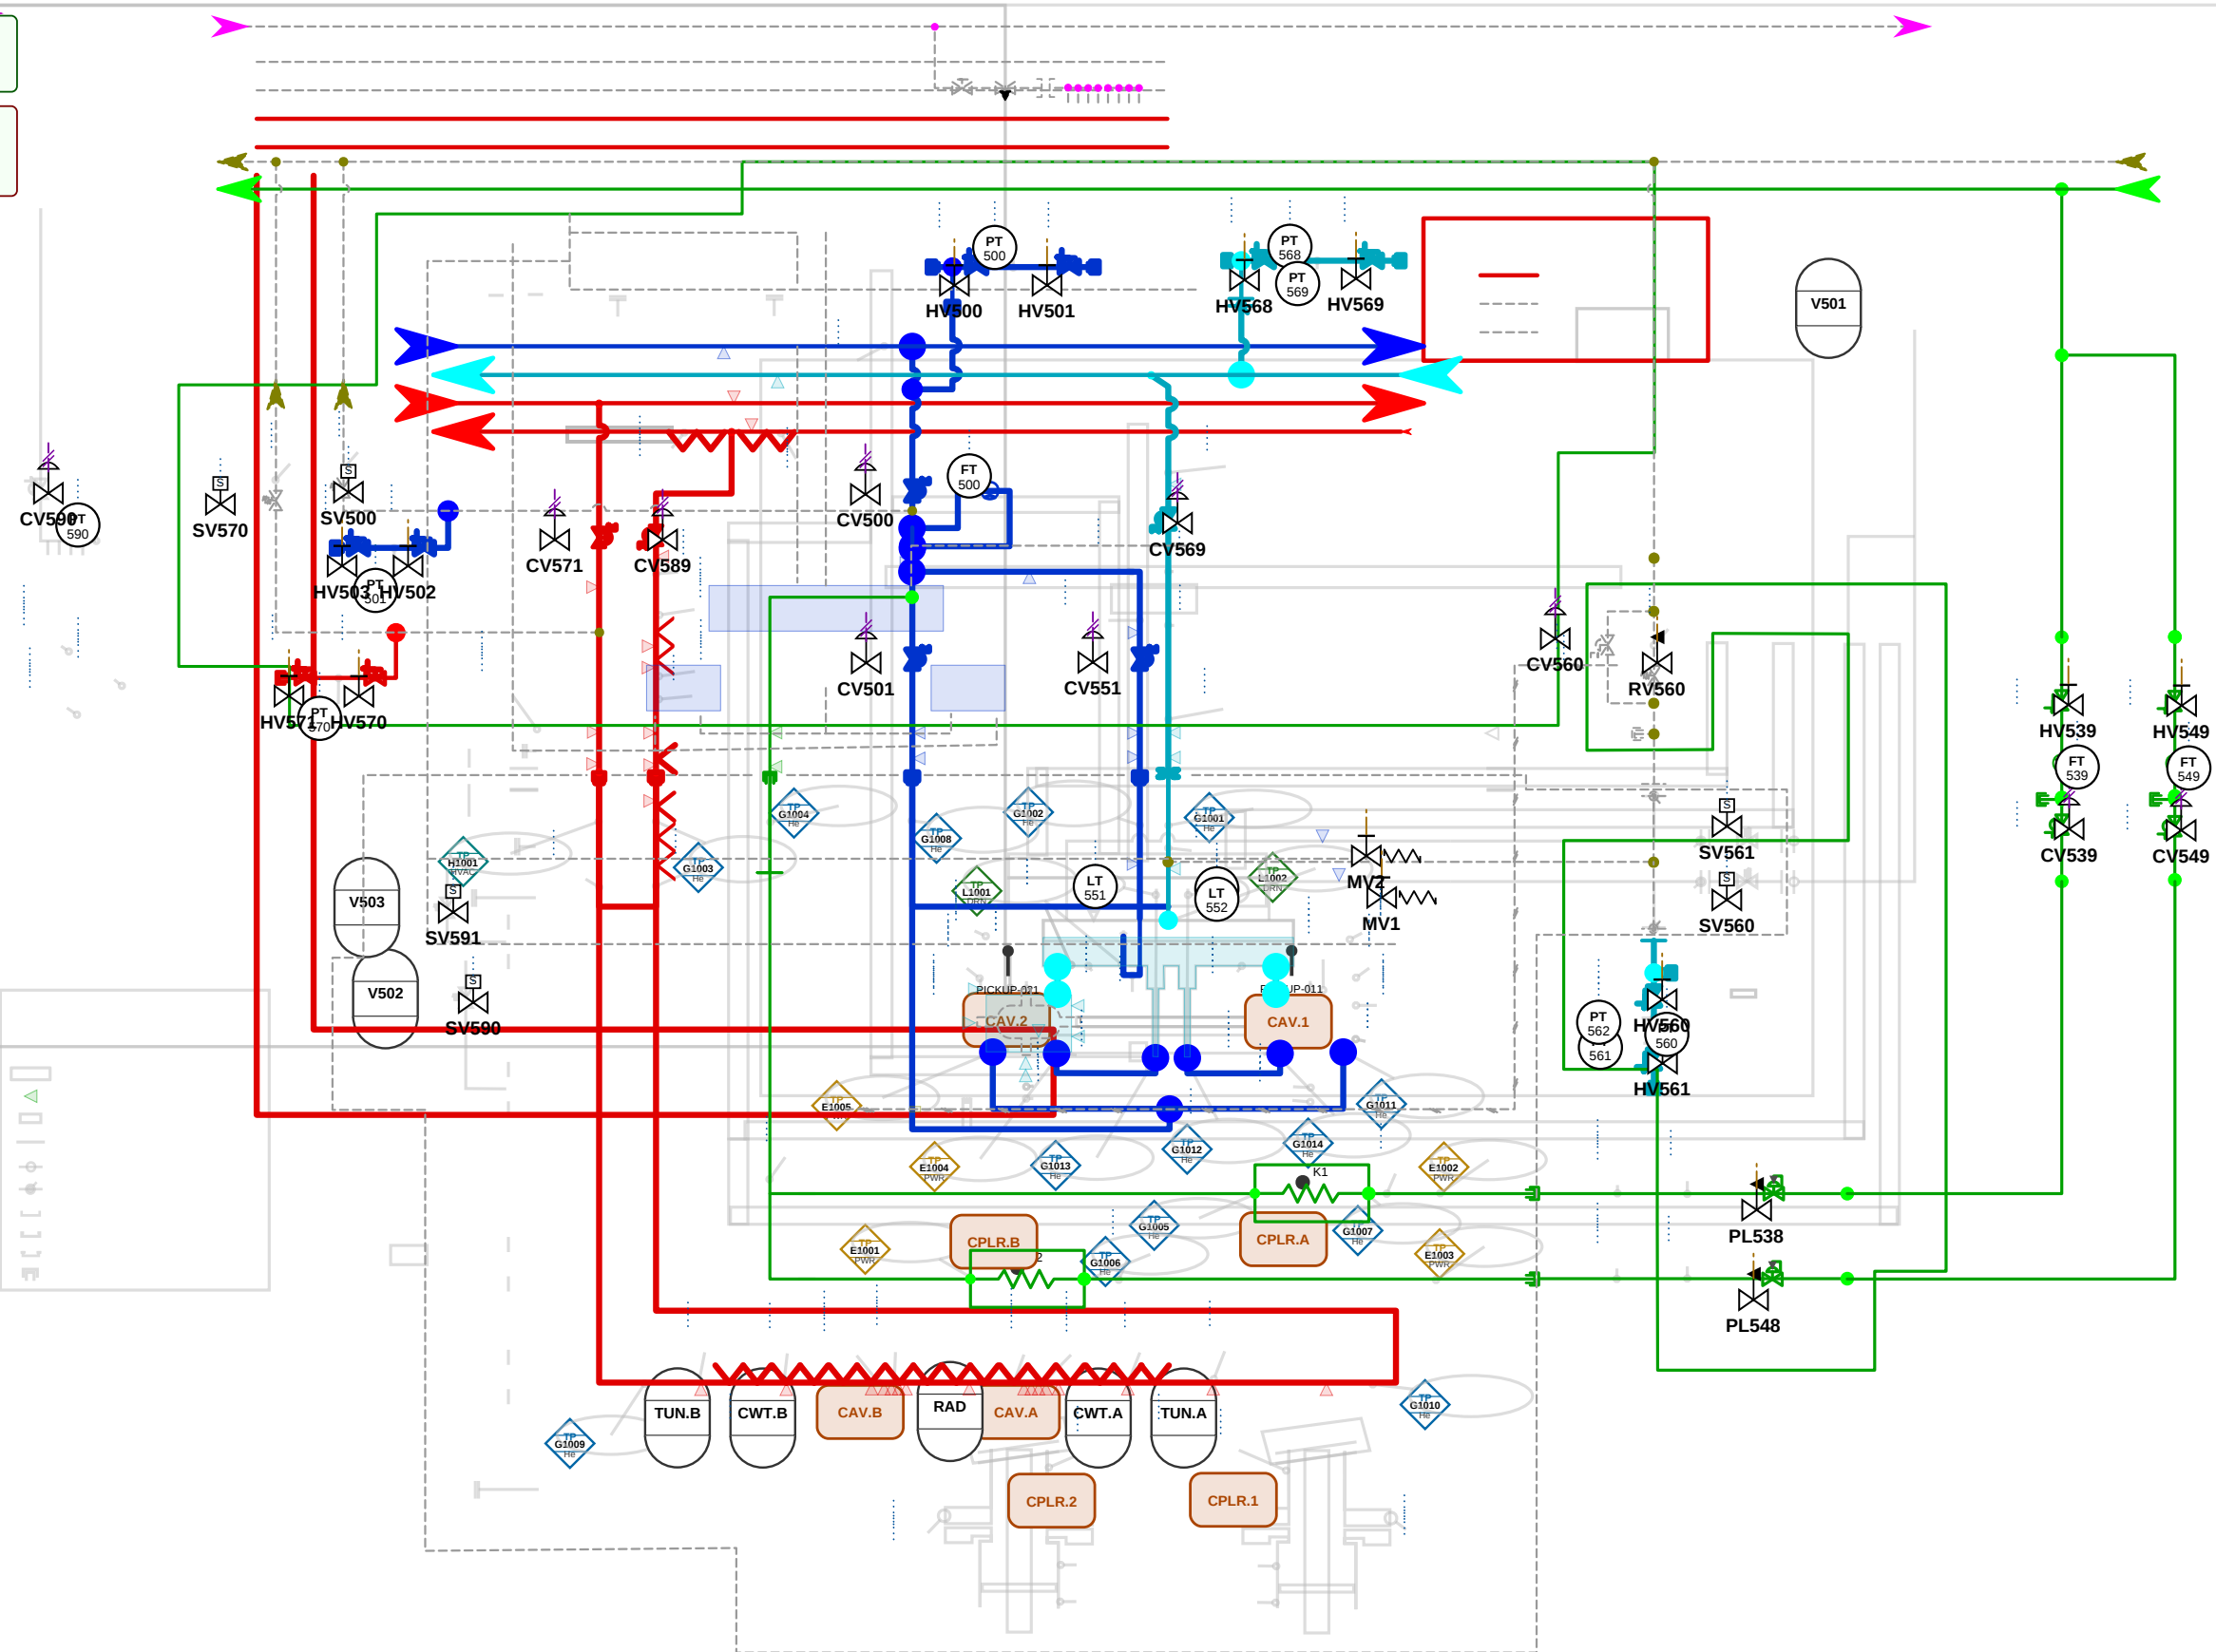

CONSULTANT Mott MacDonald Bristol, UK		CLIENT SCK CEN Boeretang 200, 2400 Mol, BE MYRRHA / MINERVA Phase 1	REVISIONS Rev	Date	Description	App'd	APPROVALS Designed QSYS Drawn ACR Checked ACR Approved PM	MINERVA CryoCell - SCK CEN QCELL / LB - Cryogenic Circuits (40 K / 4. DWG No. =NA.PS01_PFB712 MMD Proj. 411066 Scale NTS Suitability S2 - FOR ACCEPTANCE Security RESTRICTED Size / Std A3 / ISO10628 / ISA-5.1 Sheet Sheet1 of 2 - Cryogenic Variant STANDARD
		C1	2026-06	v3 refinement - layers/legibil	ACR			
		B1	2026-05	v2 split sheets	ACR			
		A1	2026-04	First issue	ACR			