


BUFFER VOLUMES
Liquid buffer: 7 L min
Vapour buffer: 5 L min

SCOPE HAND-OVER
Diamonds (TP / cat / next) mark the 'last-meter' hand-over between in-scope and out-of-scope assets.

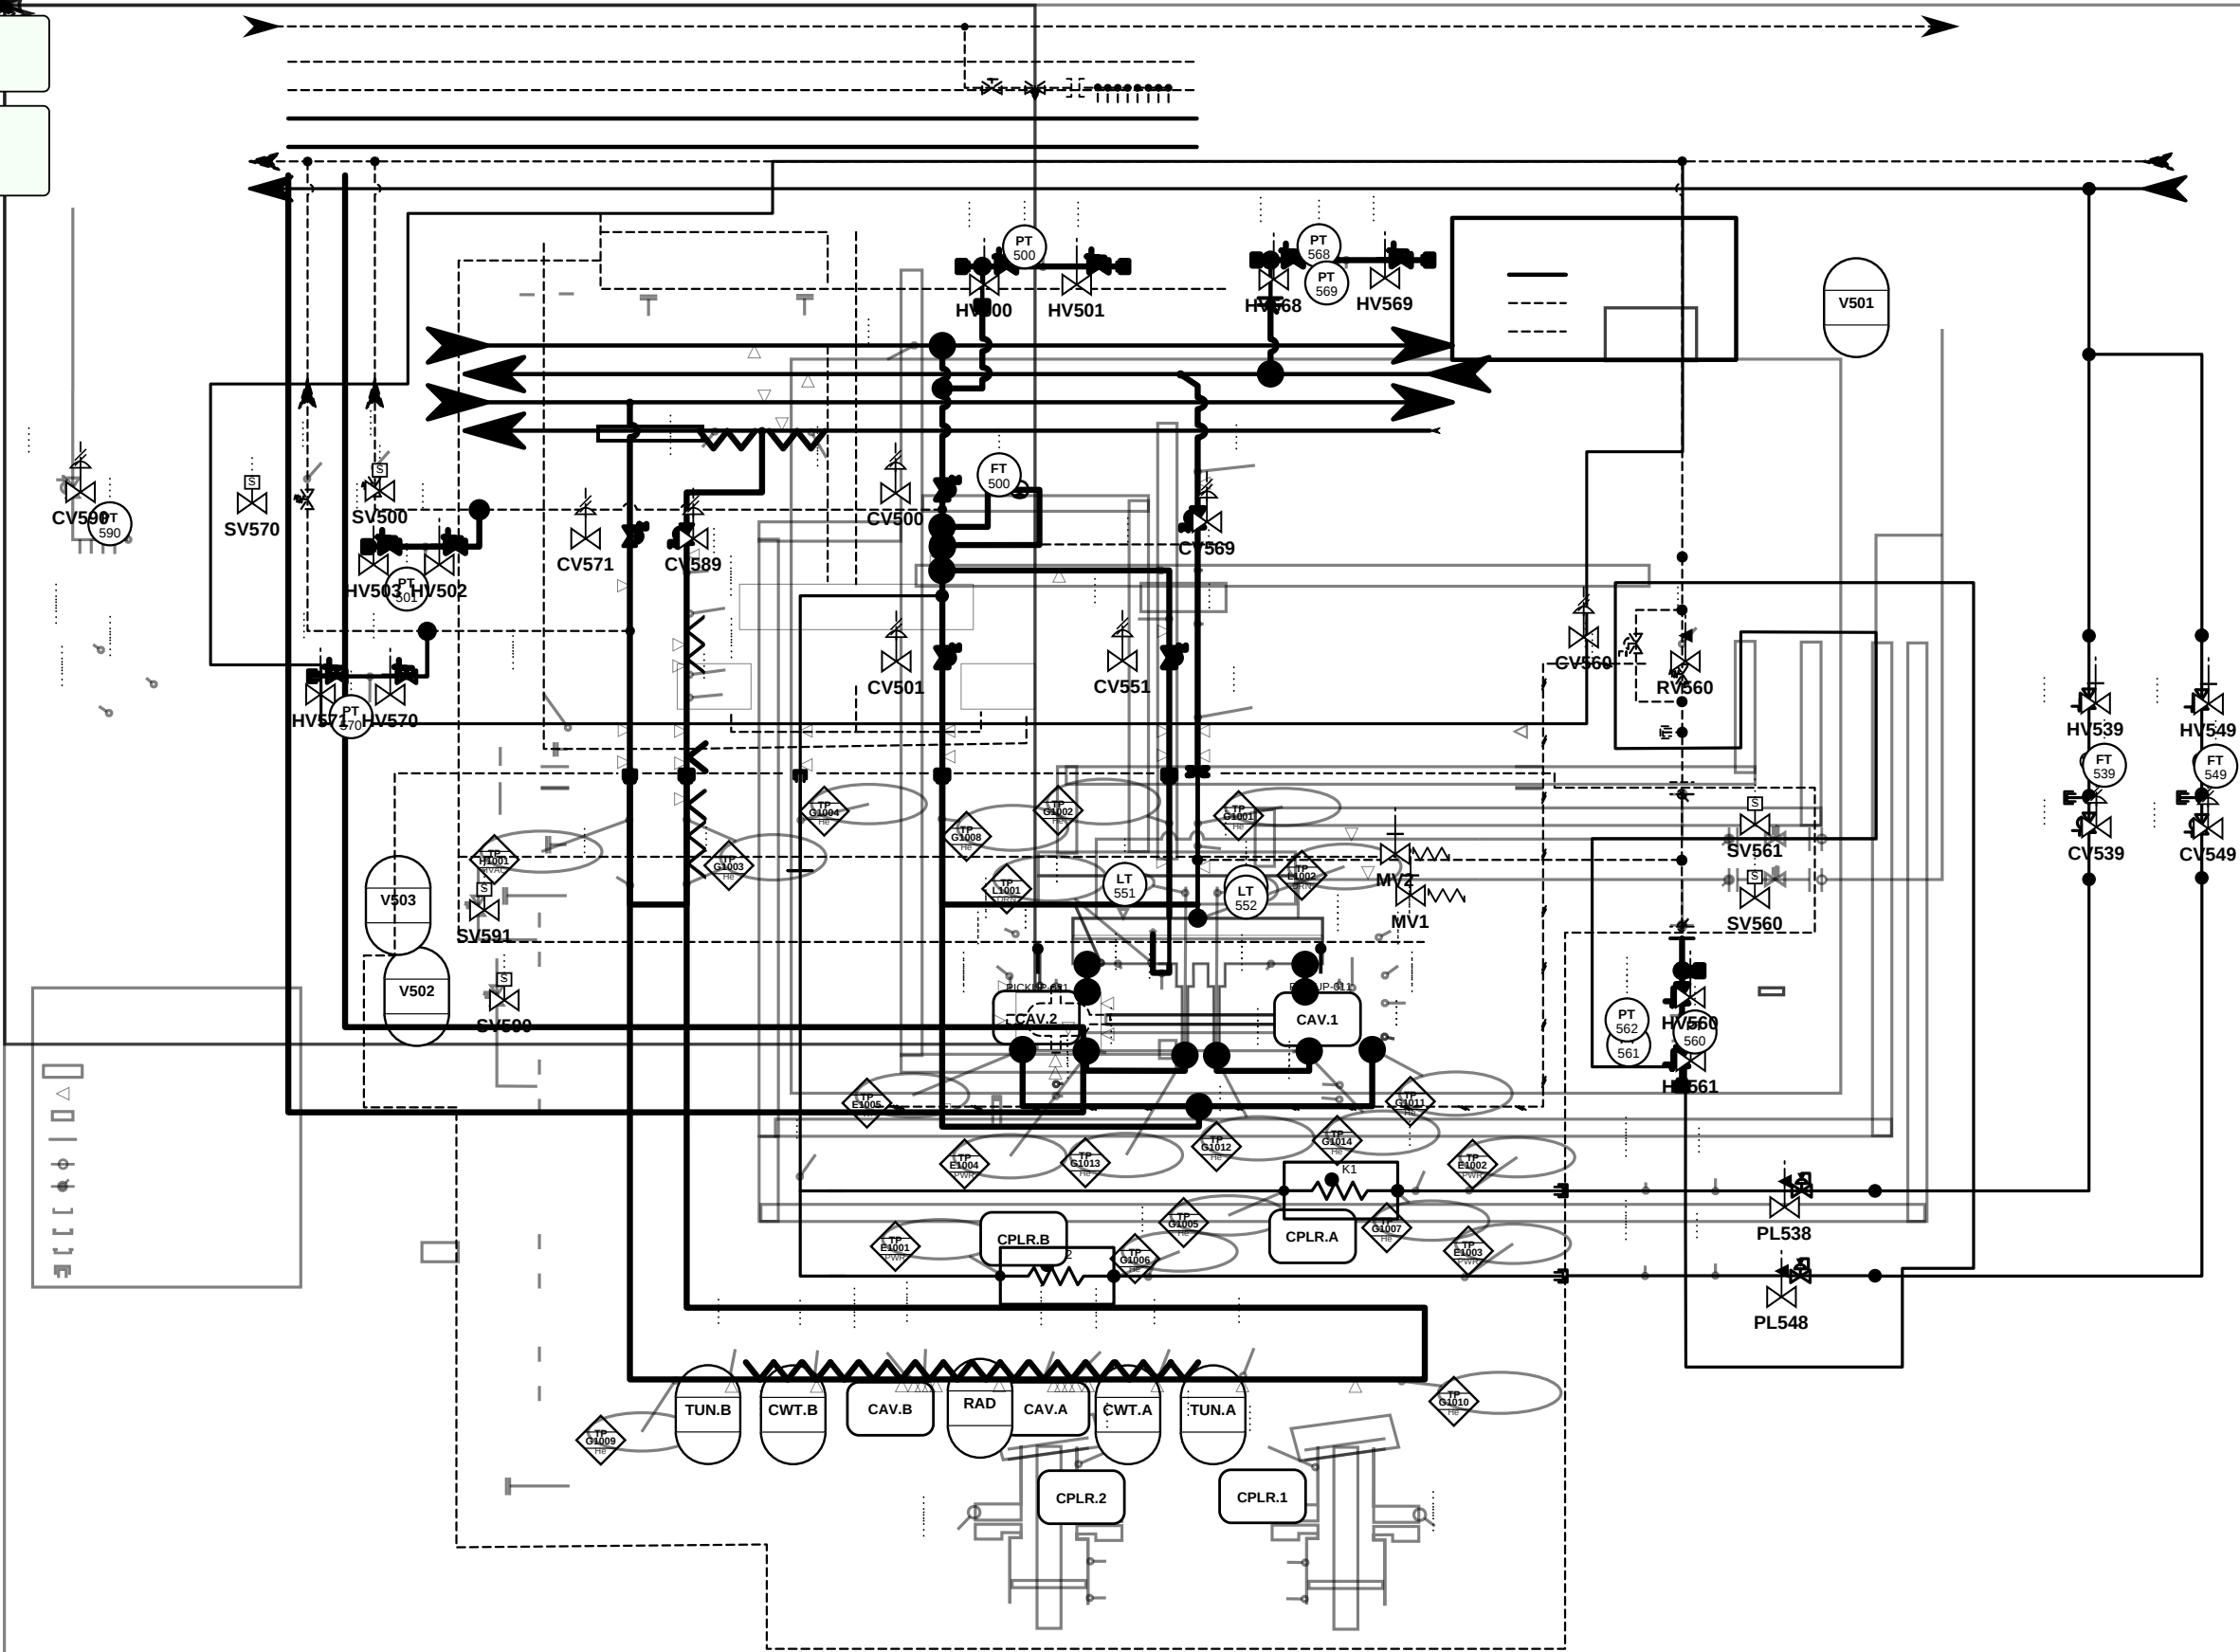

CONSULTANT Mott MacDonald Bristol, UK	CLIENT SCK CEN Boeretang 200, 2400 Mol, BE MYRRHA / MINERVA Phase 1	REVISIONS Rev Date Description	App'd	APPROVALS Designed QSYS Drawn ACR Checked ACR Approved PM	MINERVA CryoCell - SCK CEN QCELL / LB - Cryogenic Circuits (40 K / 4. DWG No. =NA.PS01_PFB712 MMD Proj. 411066 Scale NTS Suitability S2 - FOR ACCEPTANCE Security RESTRICTED Size / Std A3 / ISO10628 / ISA-5.1 Sheet Sheet1 of 2 - Cryogenic Variant STANDARD_MONO